




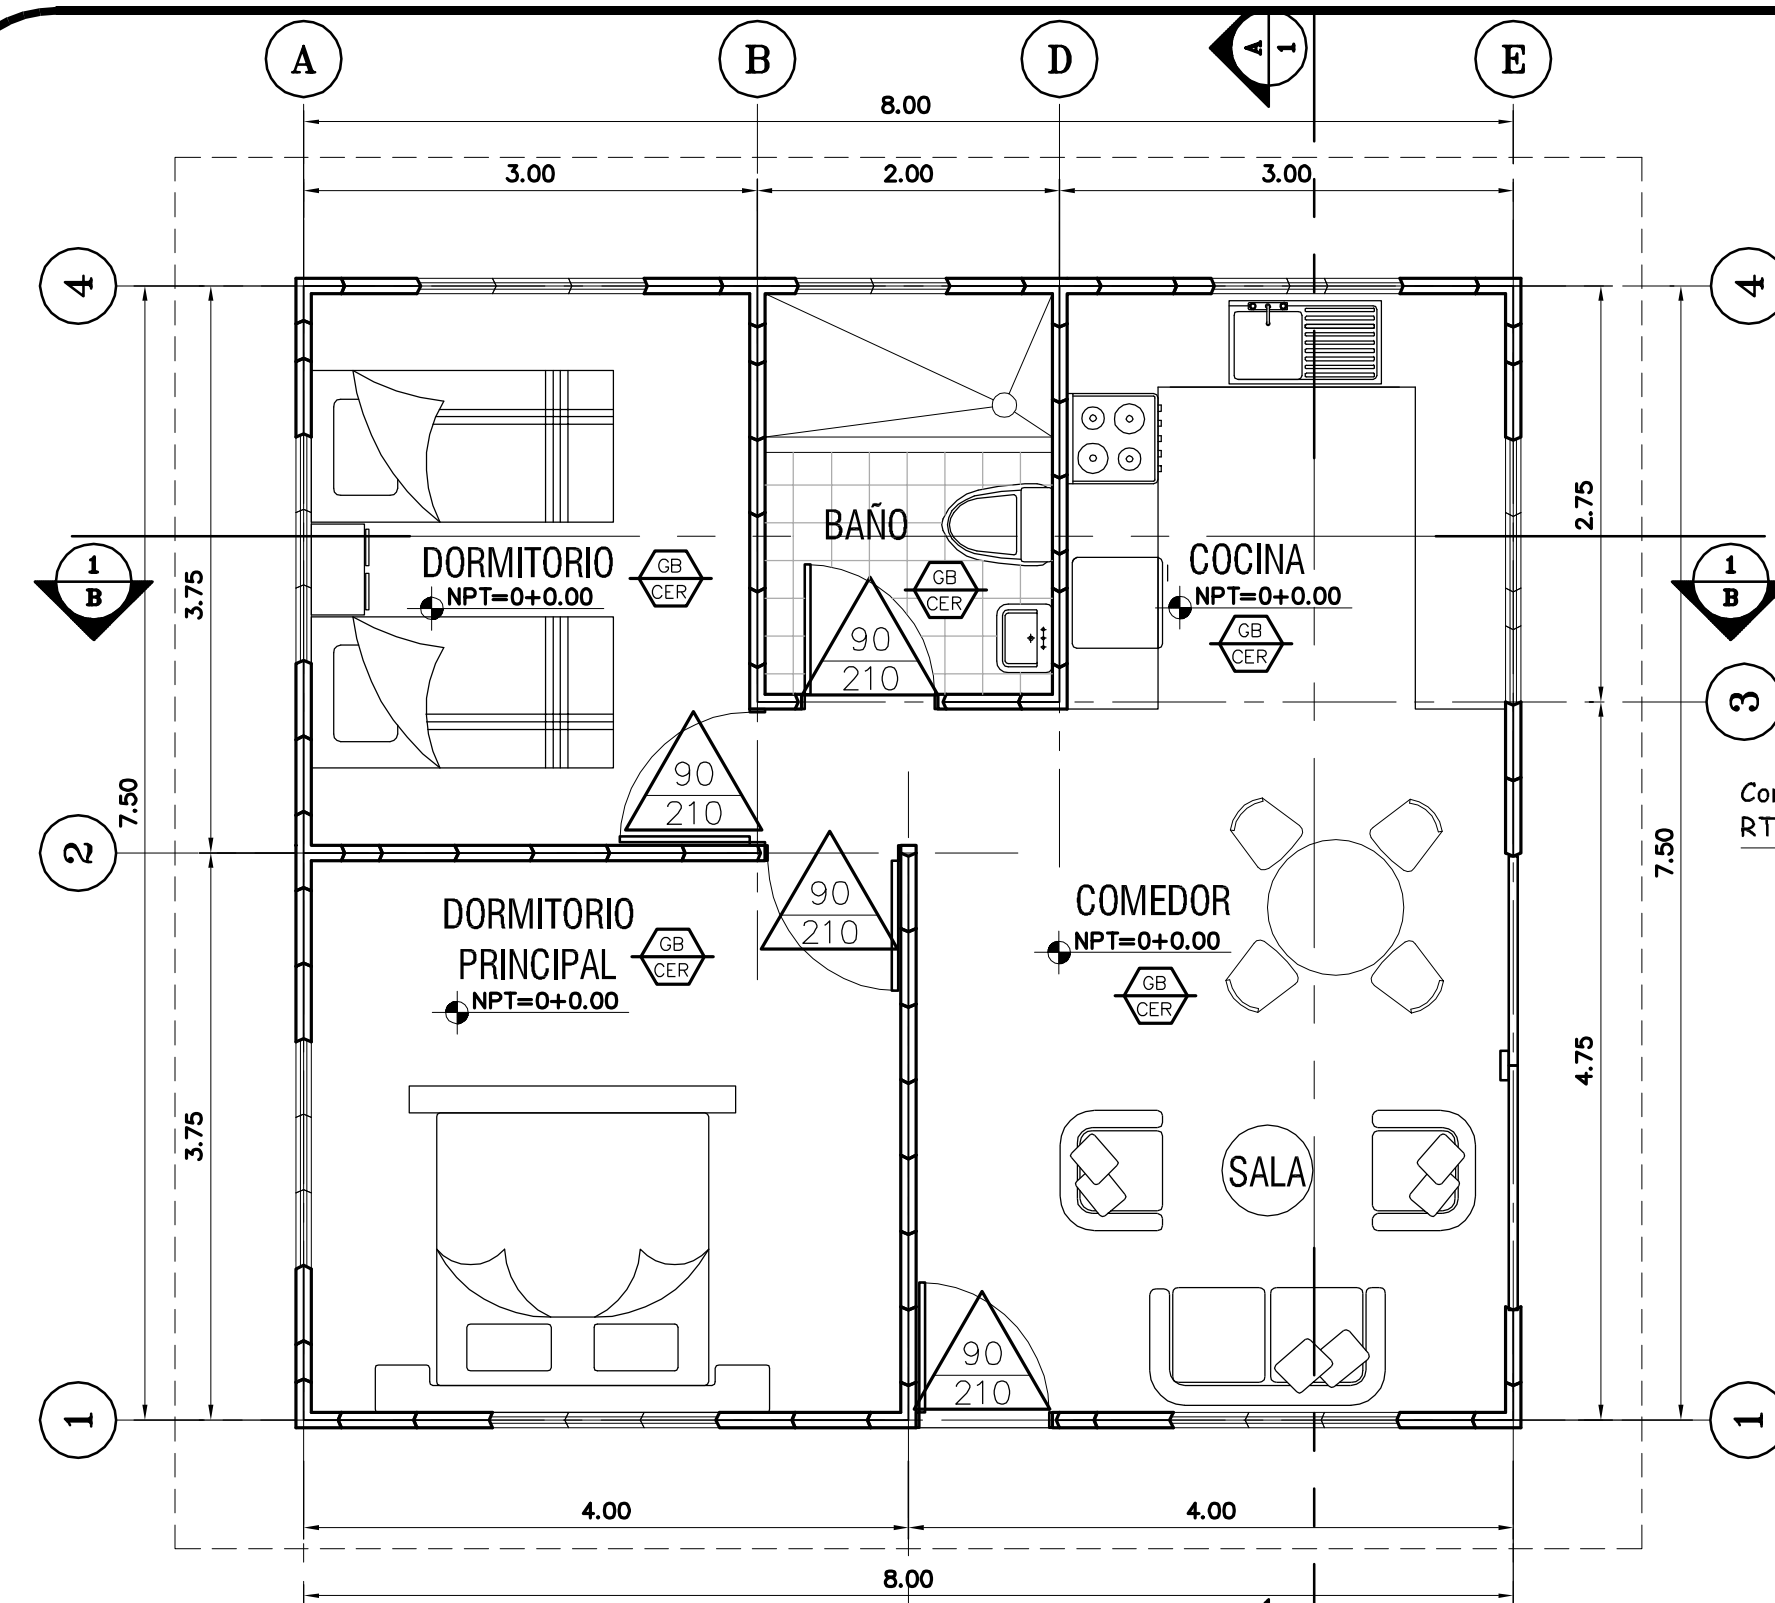


PLANTA DE DISTRIBUCION ARQUITECTONICA ESC 1:50

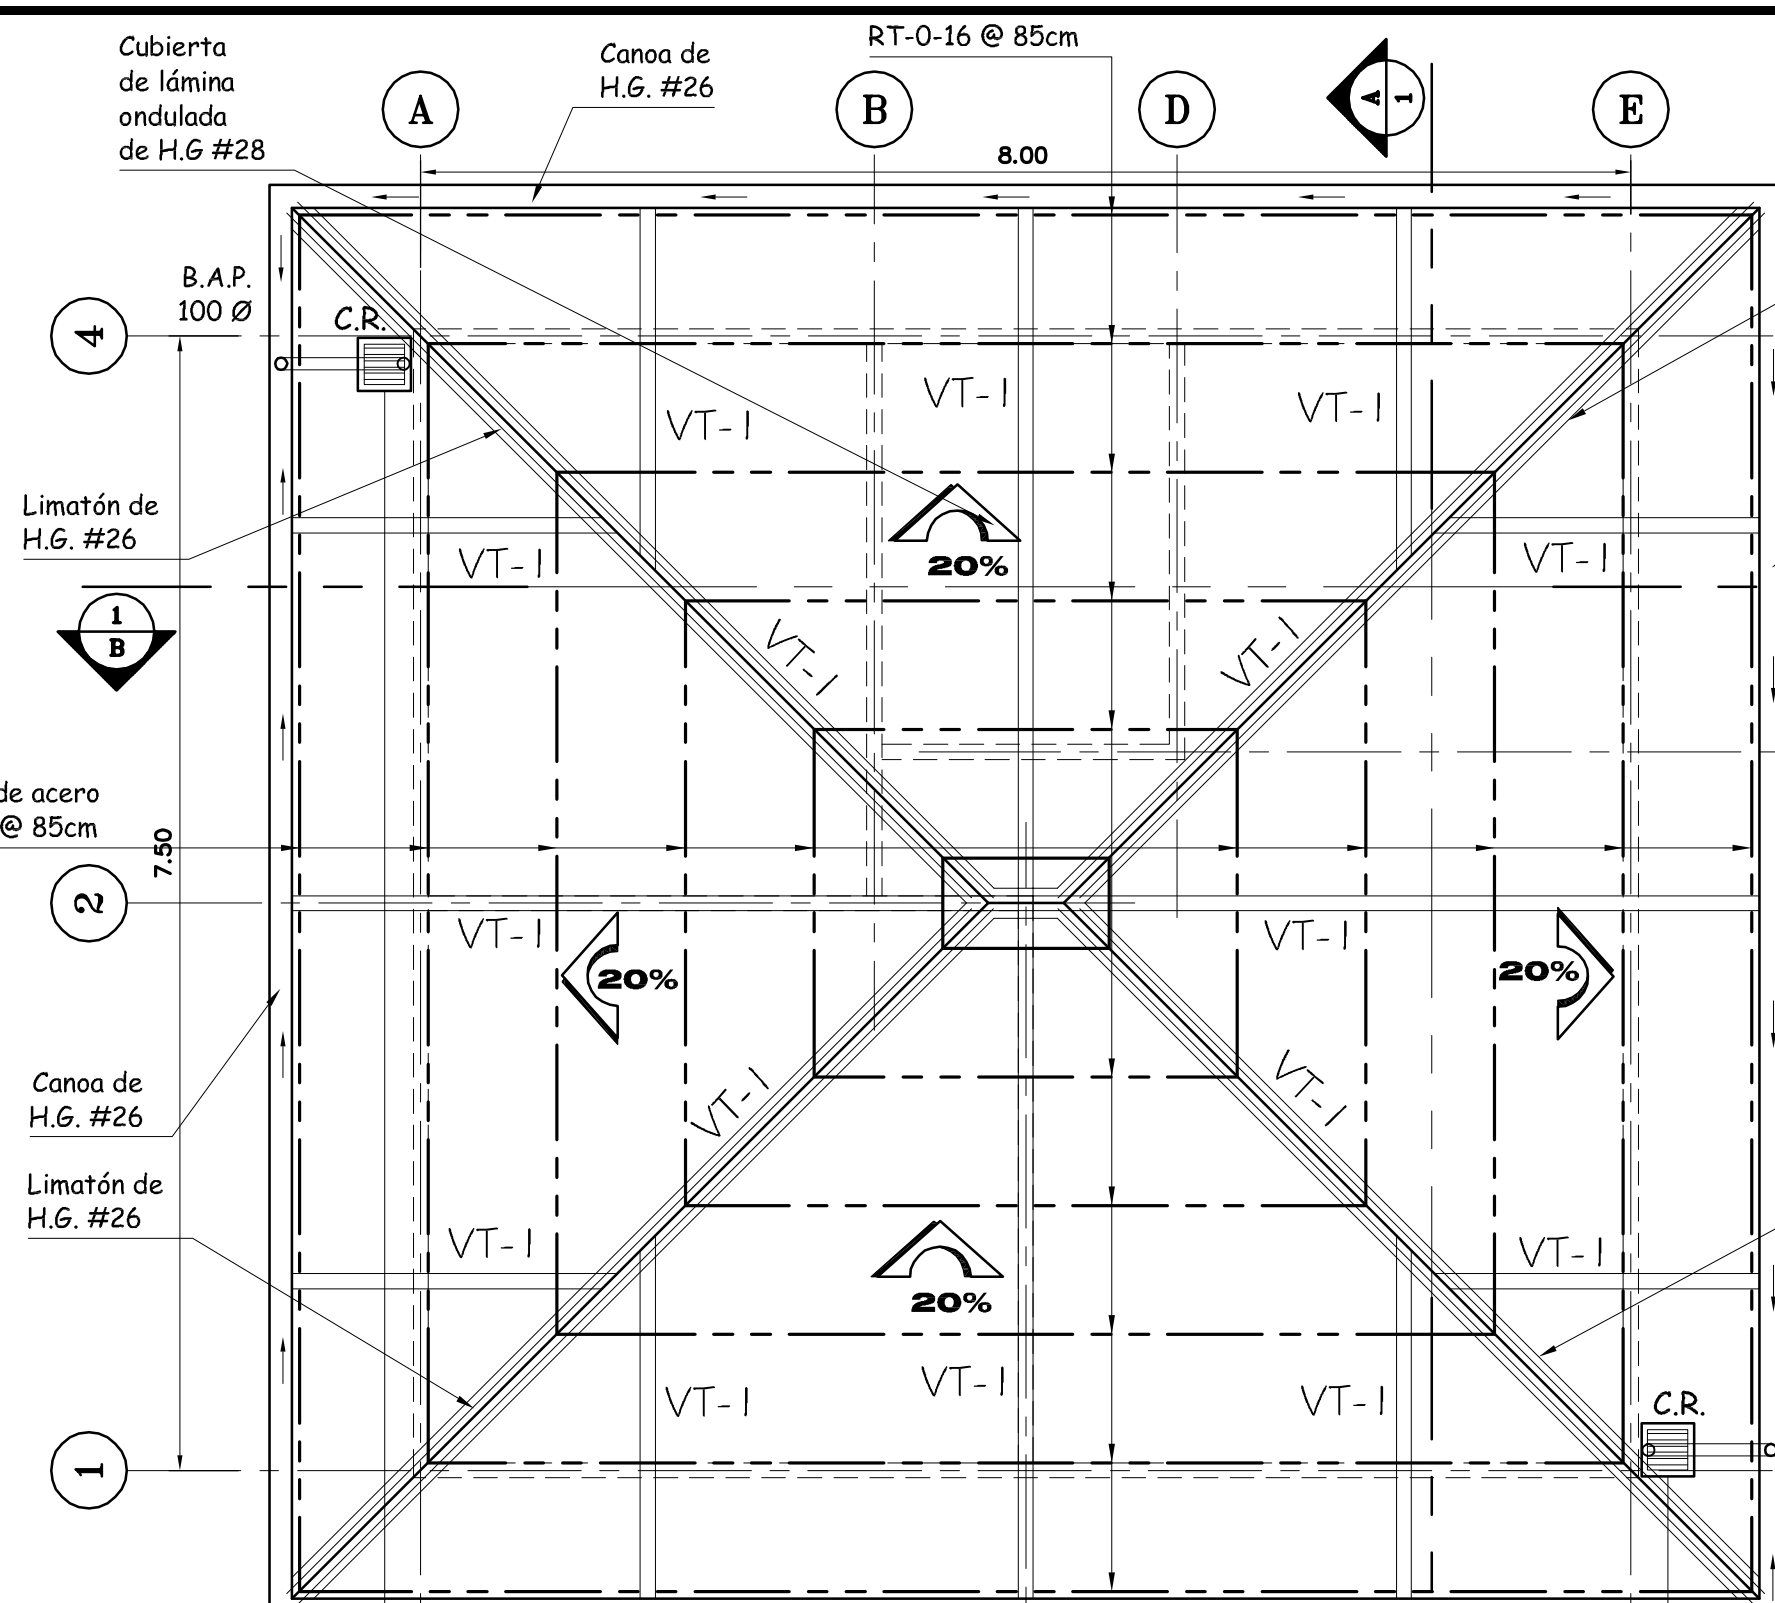


PLANTA DE TECHOS Y PLUVIALES. ESC 1:50

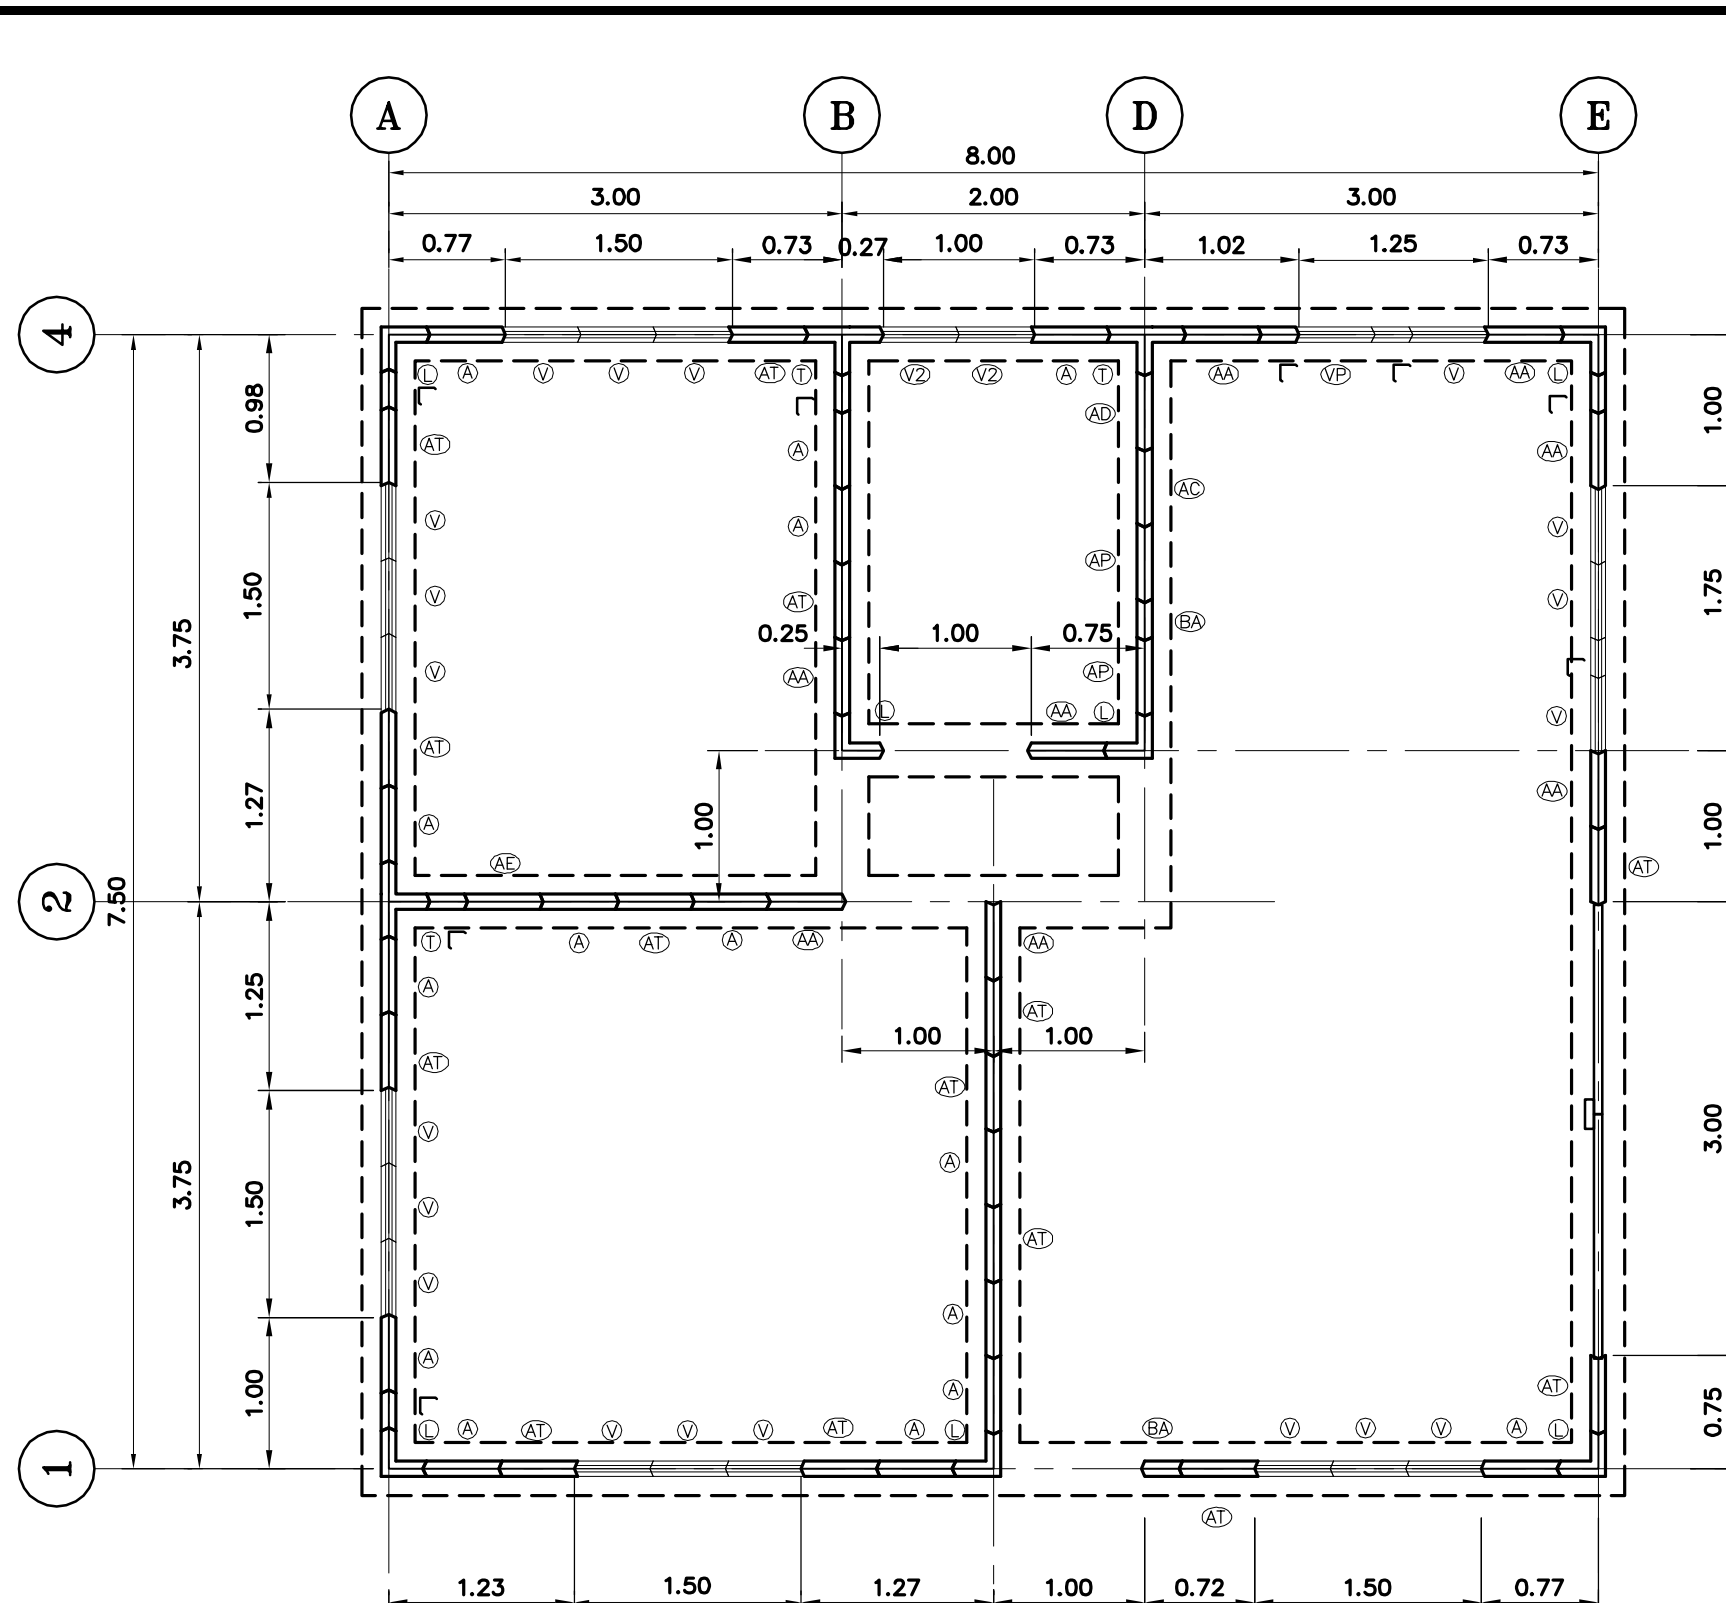


PLANTA DE FUNDACIONES Y ESTRUCTURAL ESC 1:50

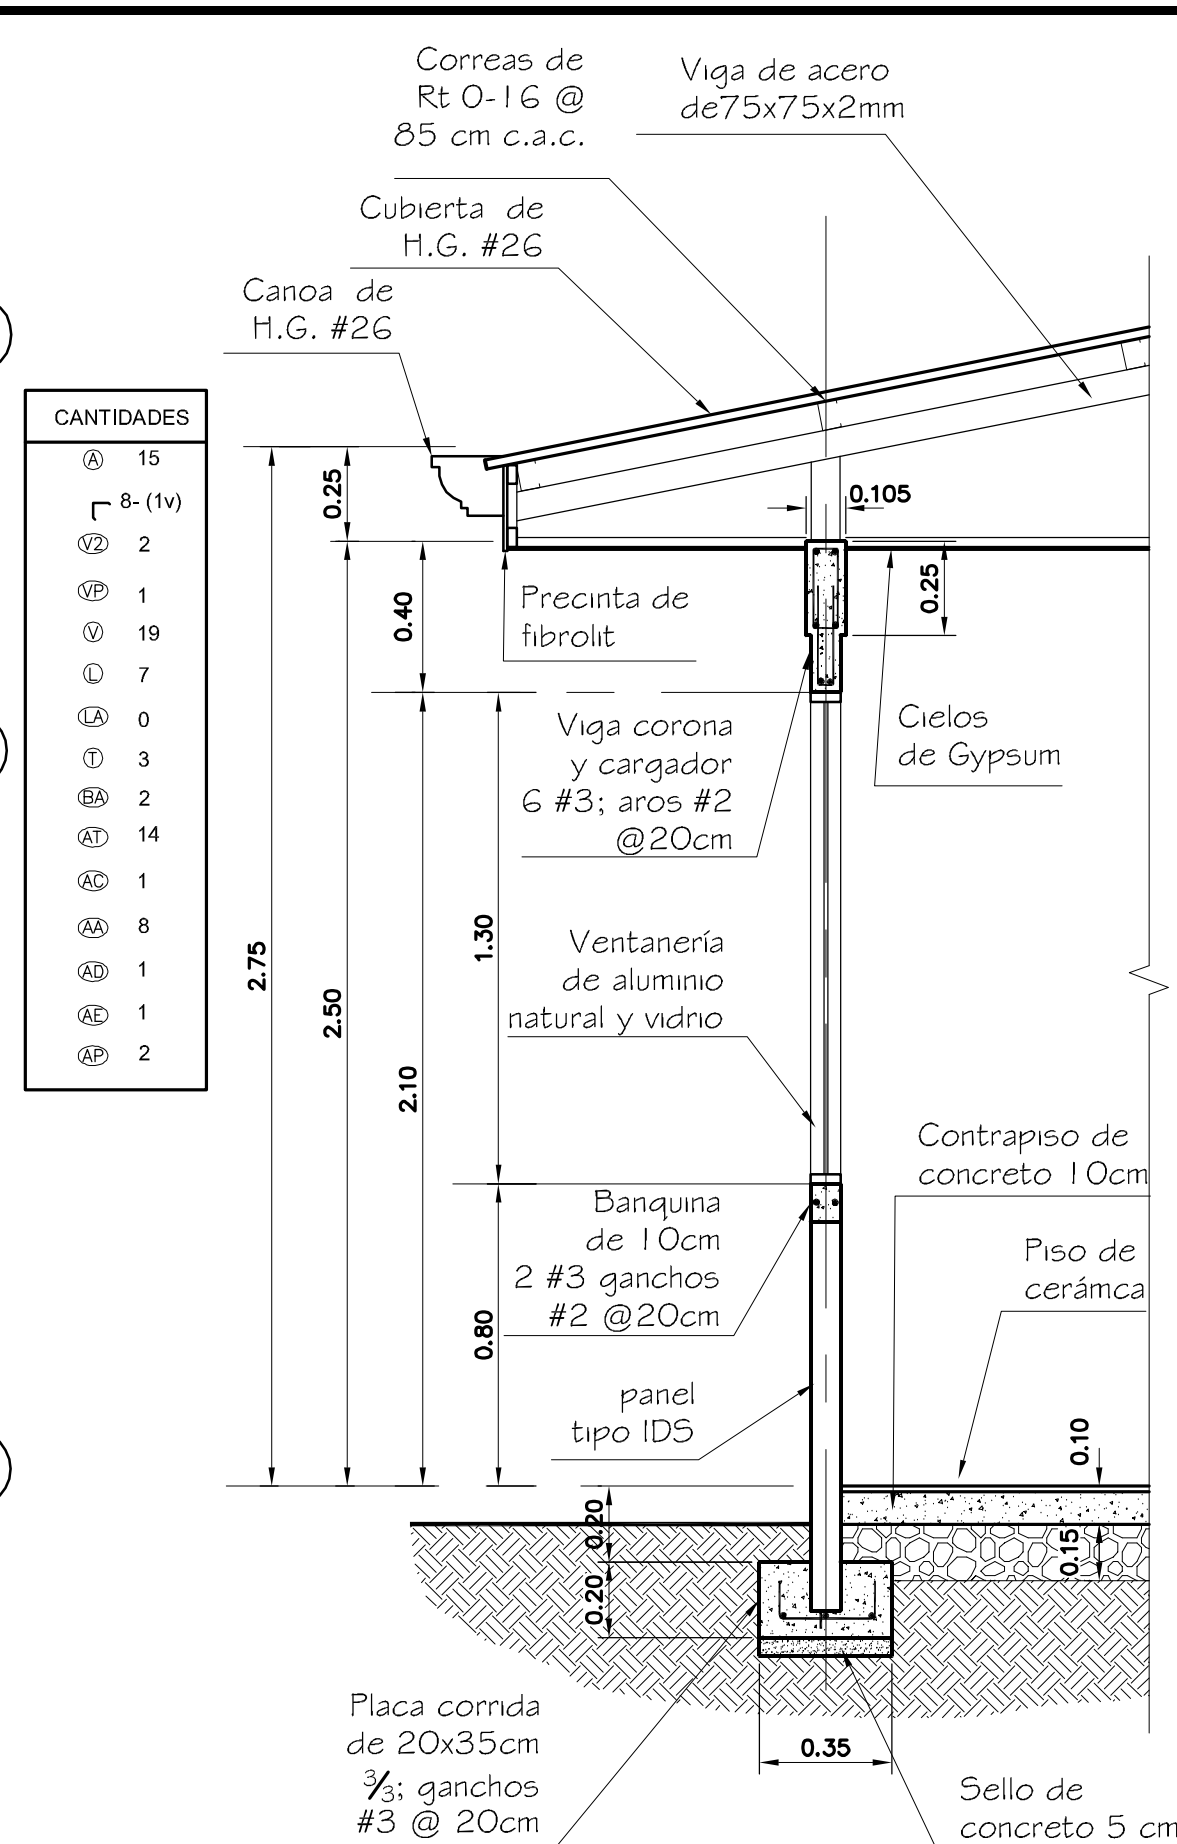


SECCION TIPICA. ESC 1:20

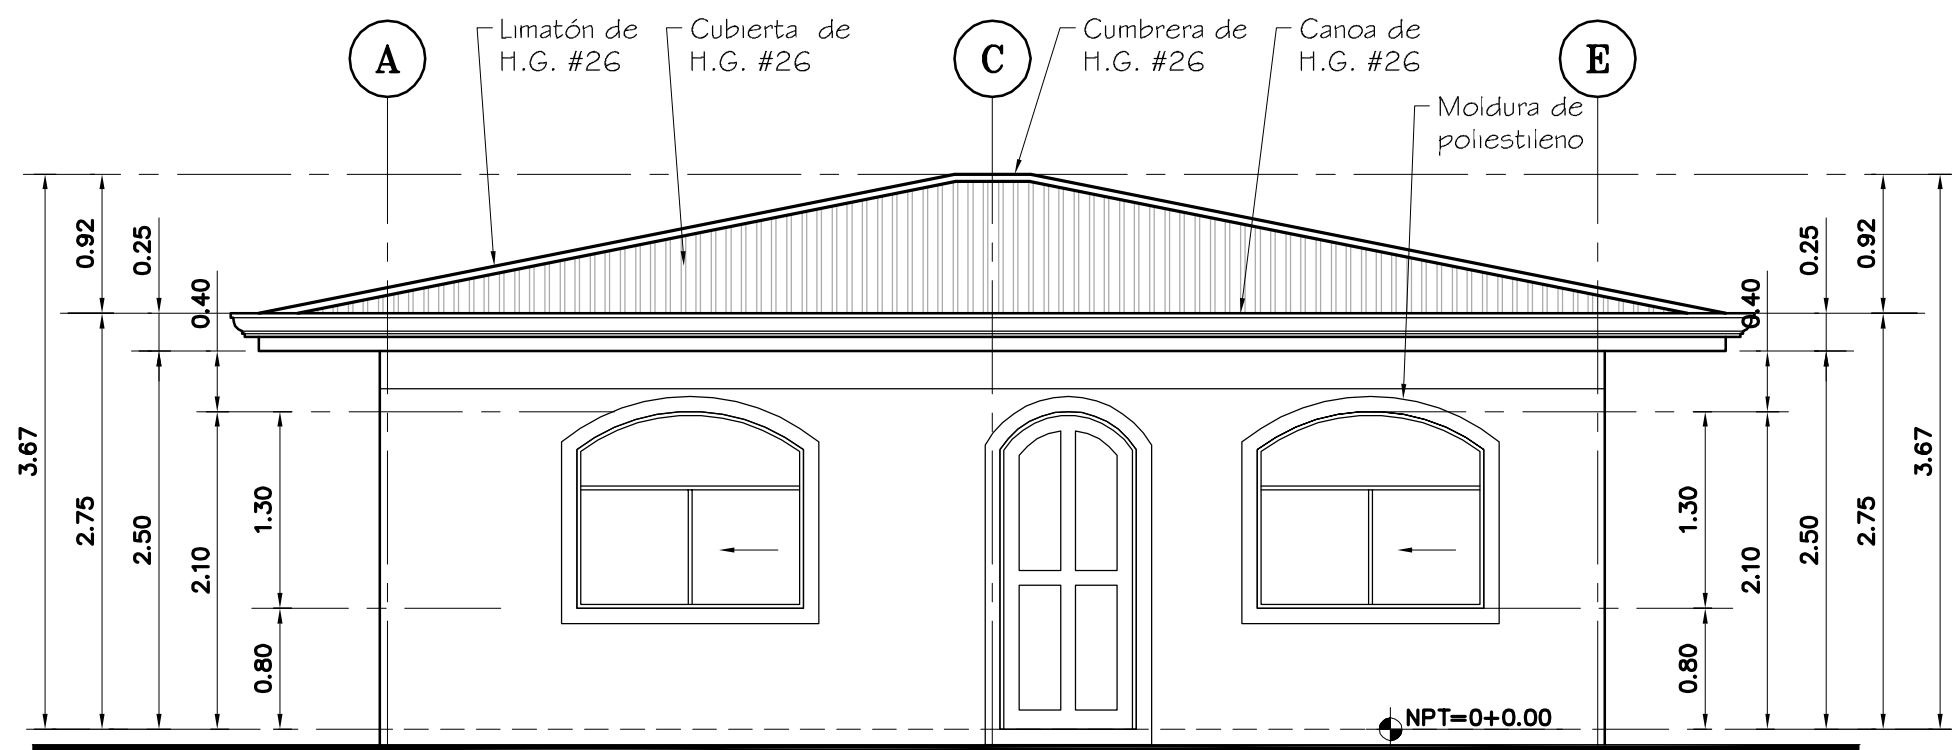


ELEVACION FRONTAL. ESC 1:50

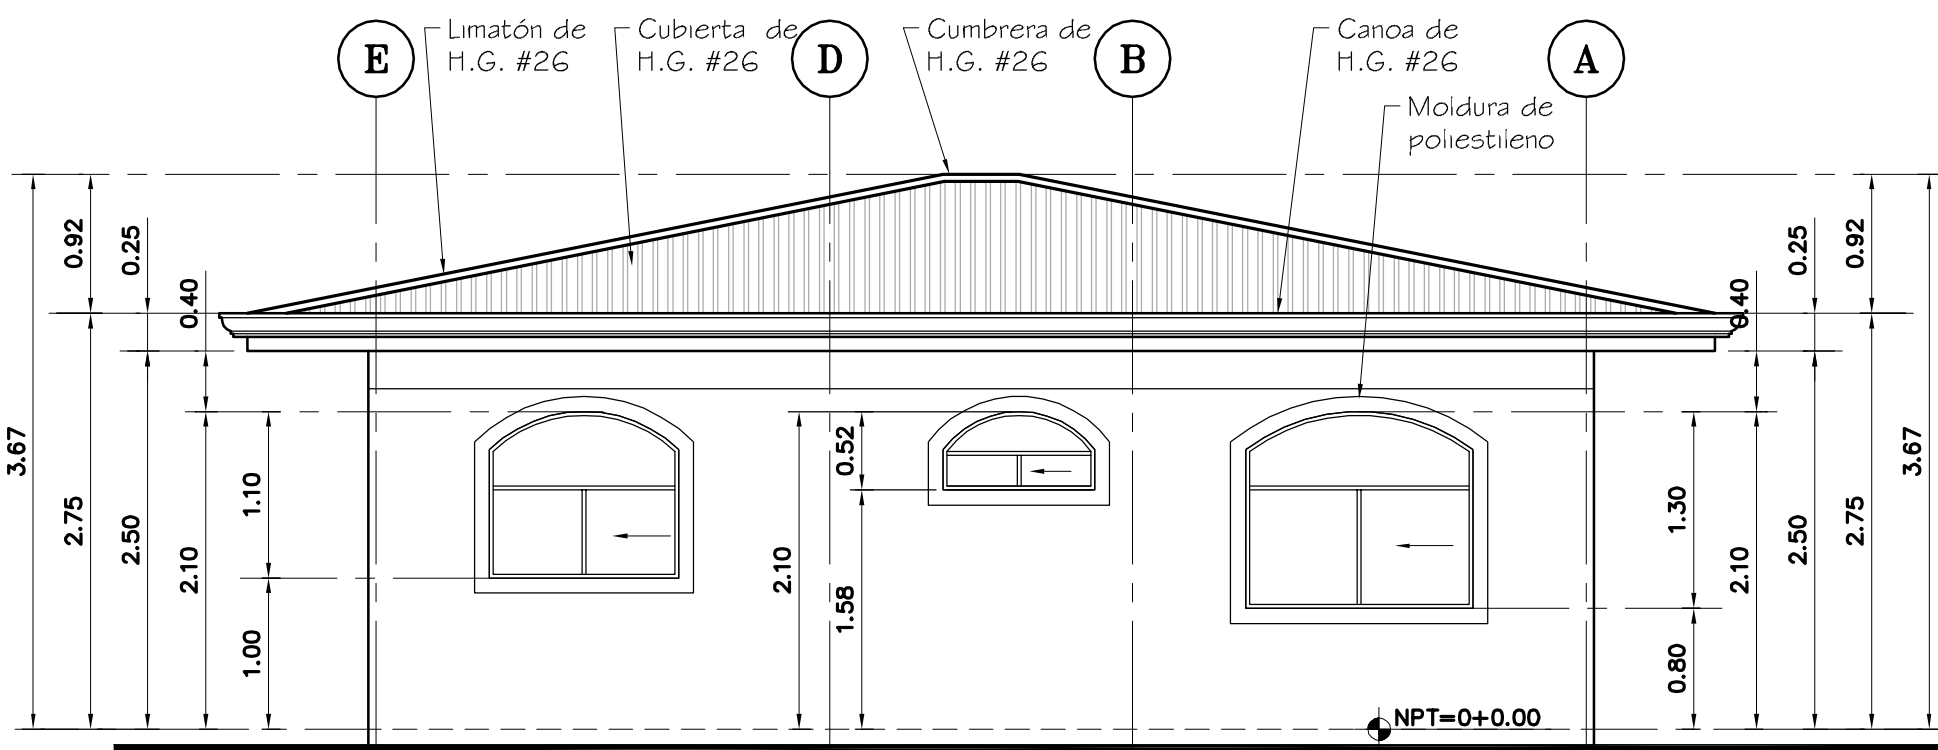


ELEVACION POSTERIOR. ESC 1:50

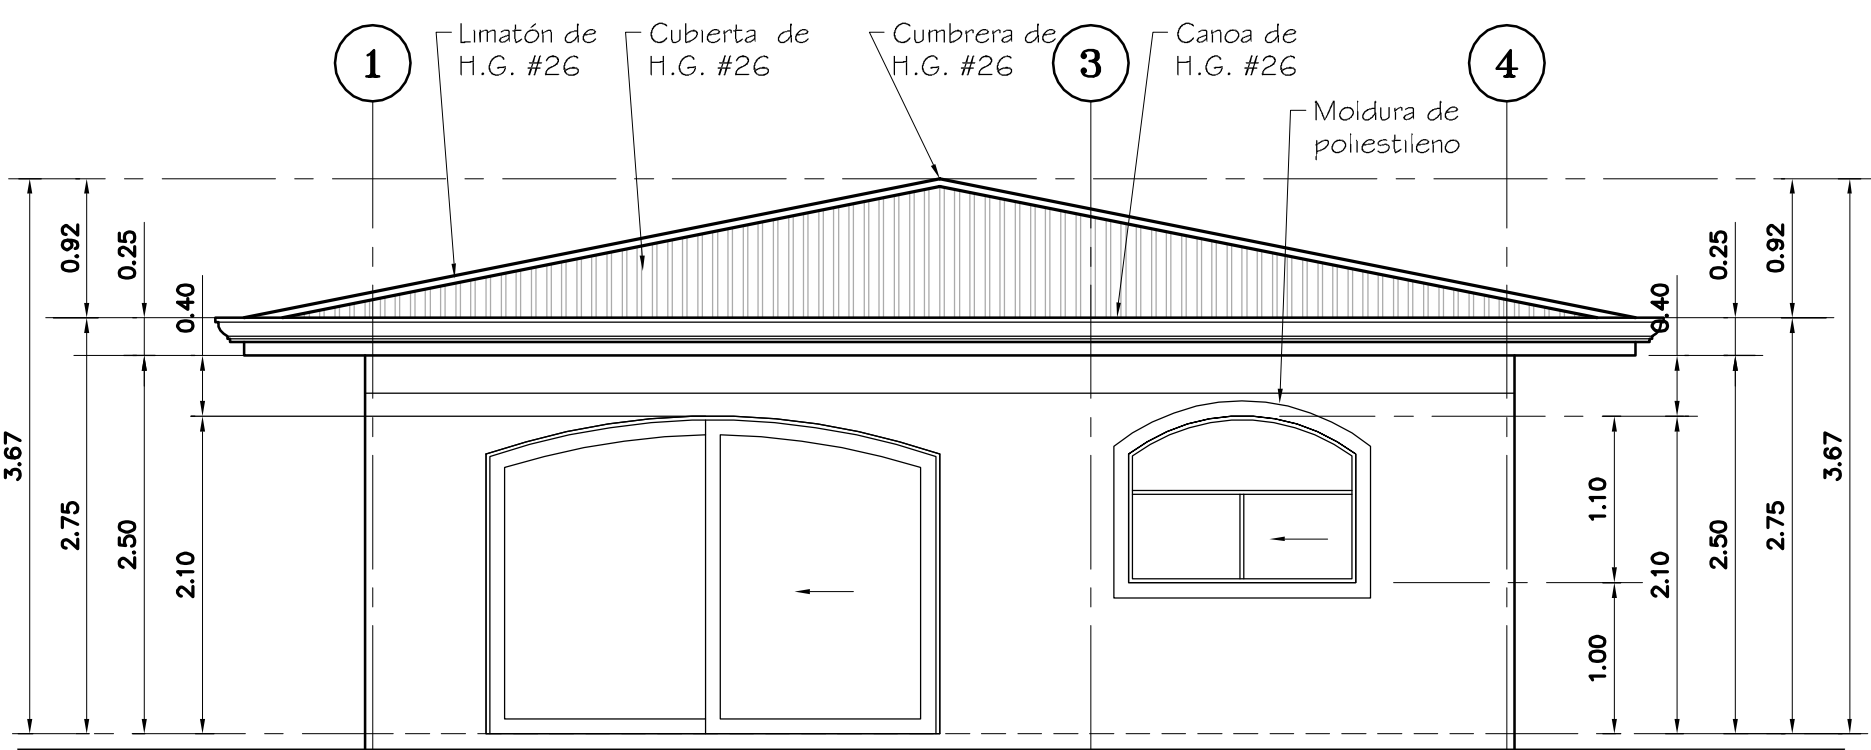


ELEVACION LATERAL DERECHA. ESC 1:50

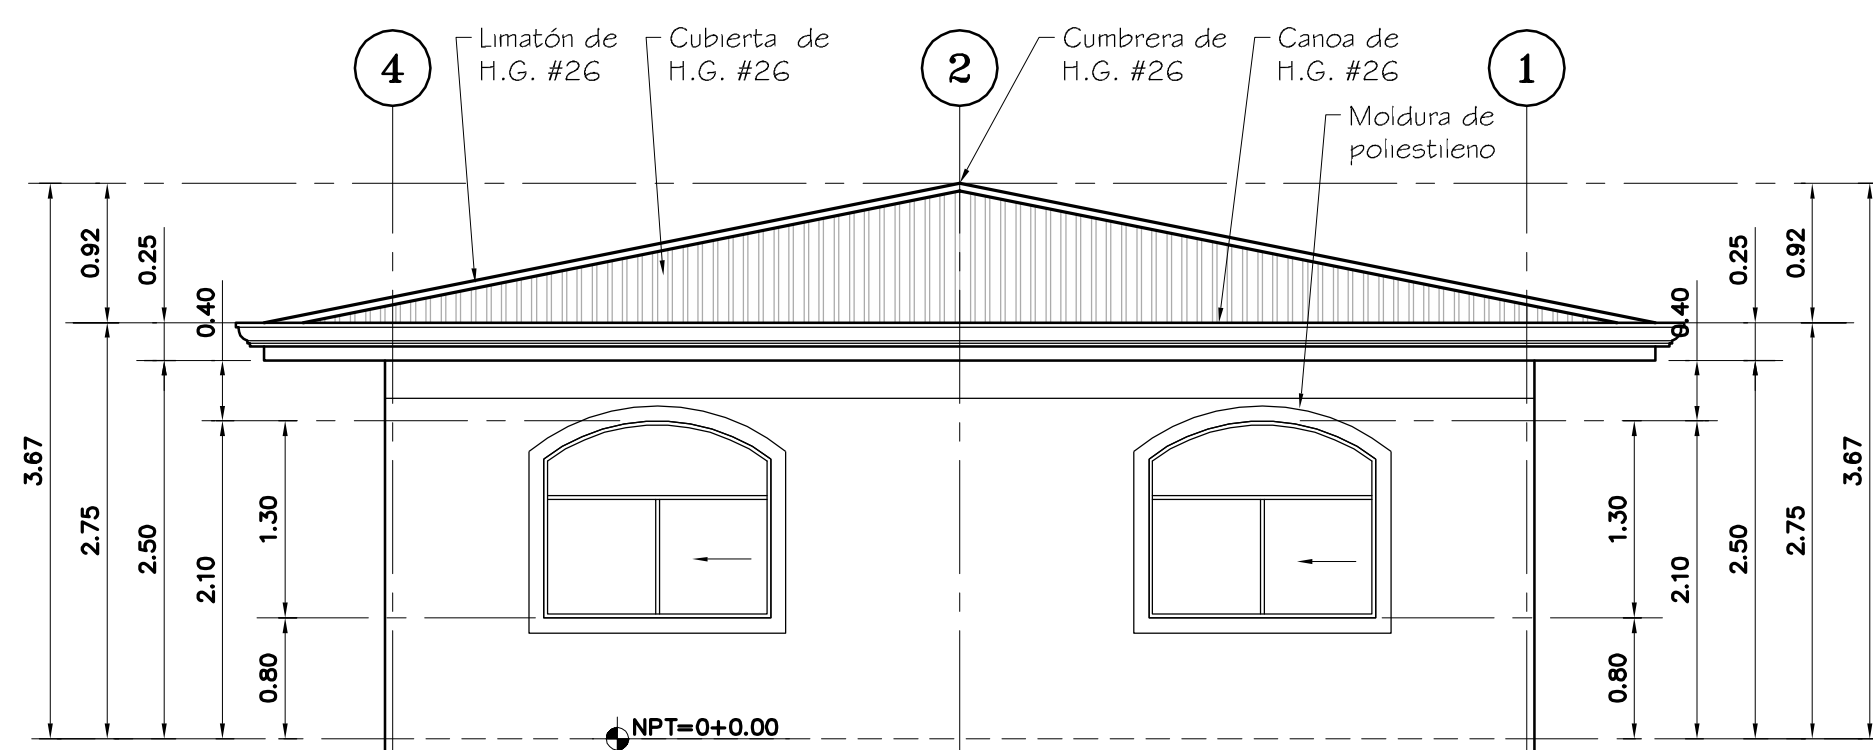

ELEVACION LATERAL IZQUIERDA. ESC 1:50

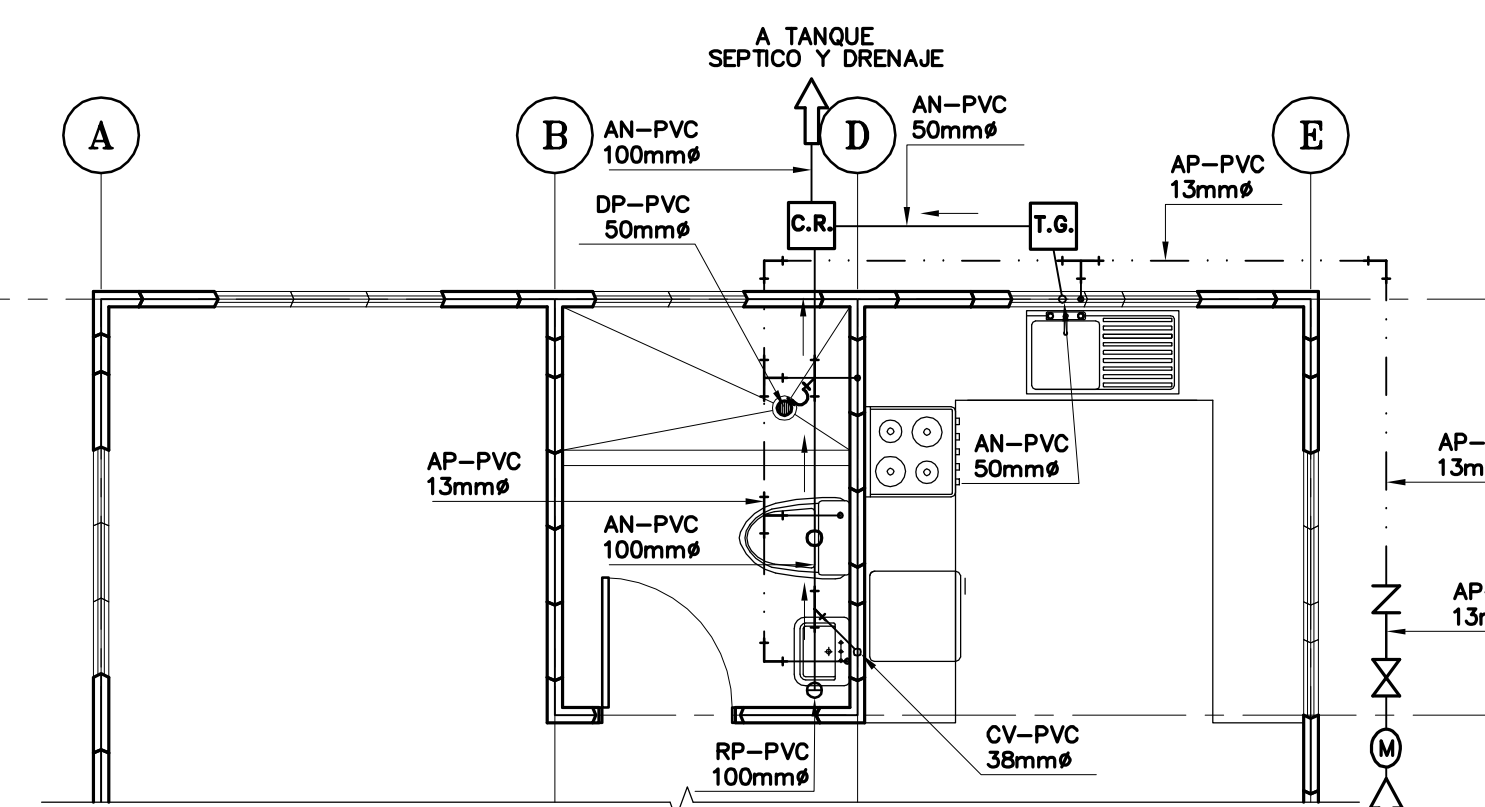


PLANTA DE INSTALACION MECANICA. ESC 1:50

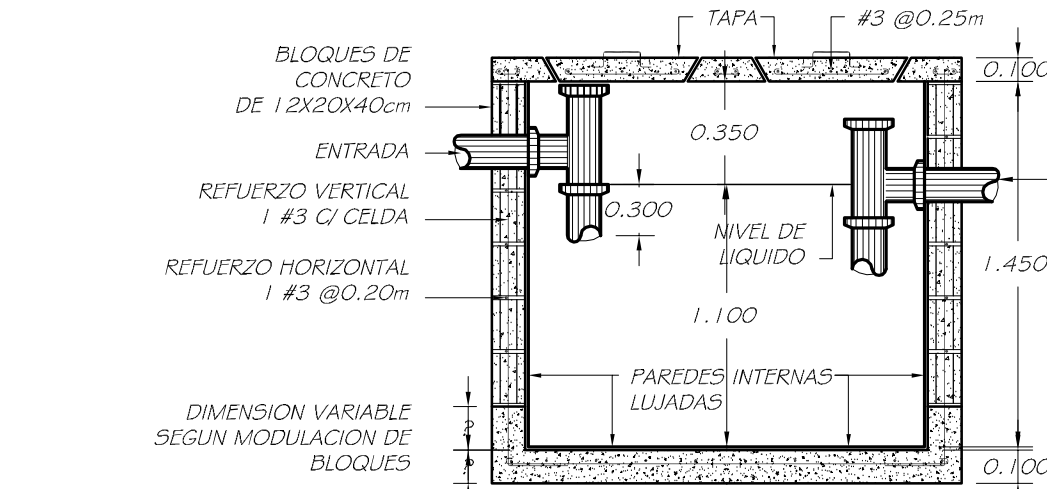


DET. DE TANQUE SEPTICO SIN ESCALA


NOTAS ESTRUCTURALES:
1.- EL CONCRETO QUE SE UTILIZARA PARA CIMENTOS, LOSAS, VIGAS Y COLUMNAS TENDRA UNA RESISTENCIA MINIMA DE 210 kg/cm².
2.- EL CONCRETO QUE SE UTILIZARA PARA SELLO TENDRA UNA RESISTENCIA MINIMA DE 105 kg/cm².
3.- EL CONCRETO QUE SE UTILIZARA PARA LOSA DE CONTRAPISO Y ACERAS TENDRA UNA RESISTENCIA MINIMA DE 175 kg/cm².
4.- EL ACERO A USAR SERA SEGUN ASTM A 615 G 40.
5.- TODOS LOS ANCLAJES DE VARIAS DIBERAN TENER UN GANCHO STANDARD CON BRAZO DE 15cm MINIMO (PARA VARILLA #2, #3, #4).
6.- LA SUSTITUCION DE TERRENO DEBERA HACERSE CON LASTRE COMPACTADO EN CAPAS NO MAYORES A LOS 20cm Y UNA COMPACTACION DEL 95% DE LA PRUEBA PROCTOR STANDARD.

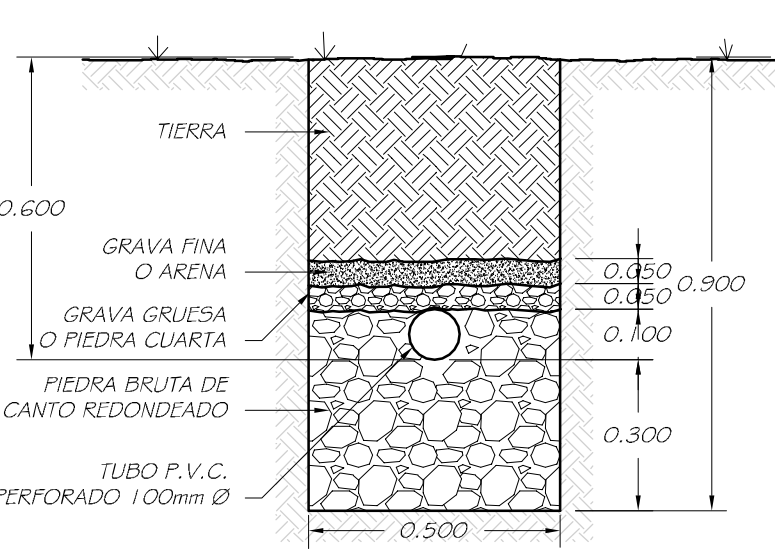


DET. DE DRENAJE ESC 1:15

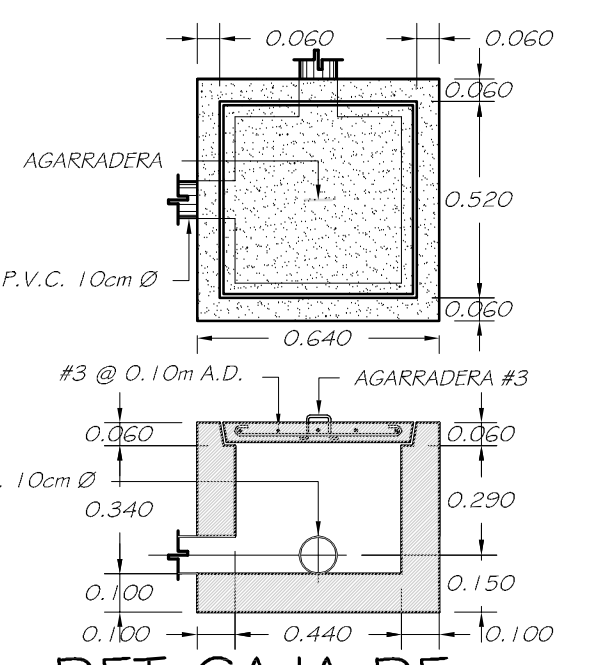


DET. CAJA DE REGISTRO ESC 1:20

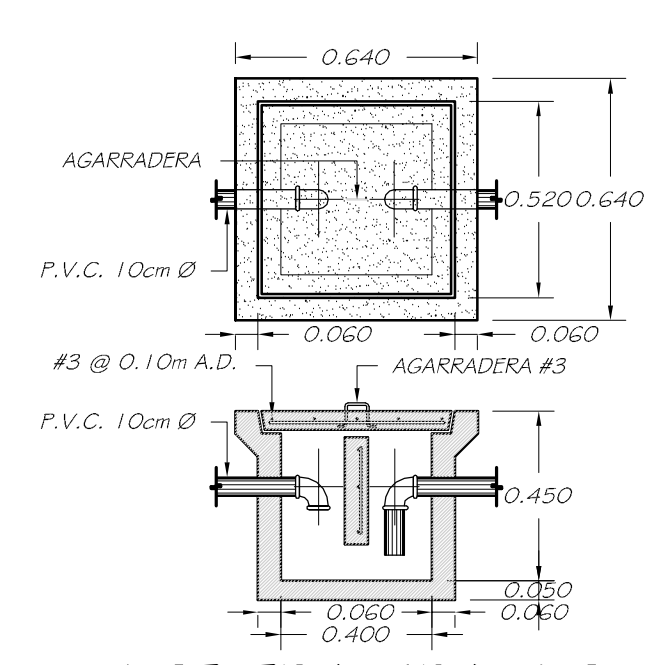

DET. TRAMPA DE GRASA ESC 1:20

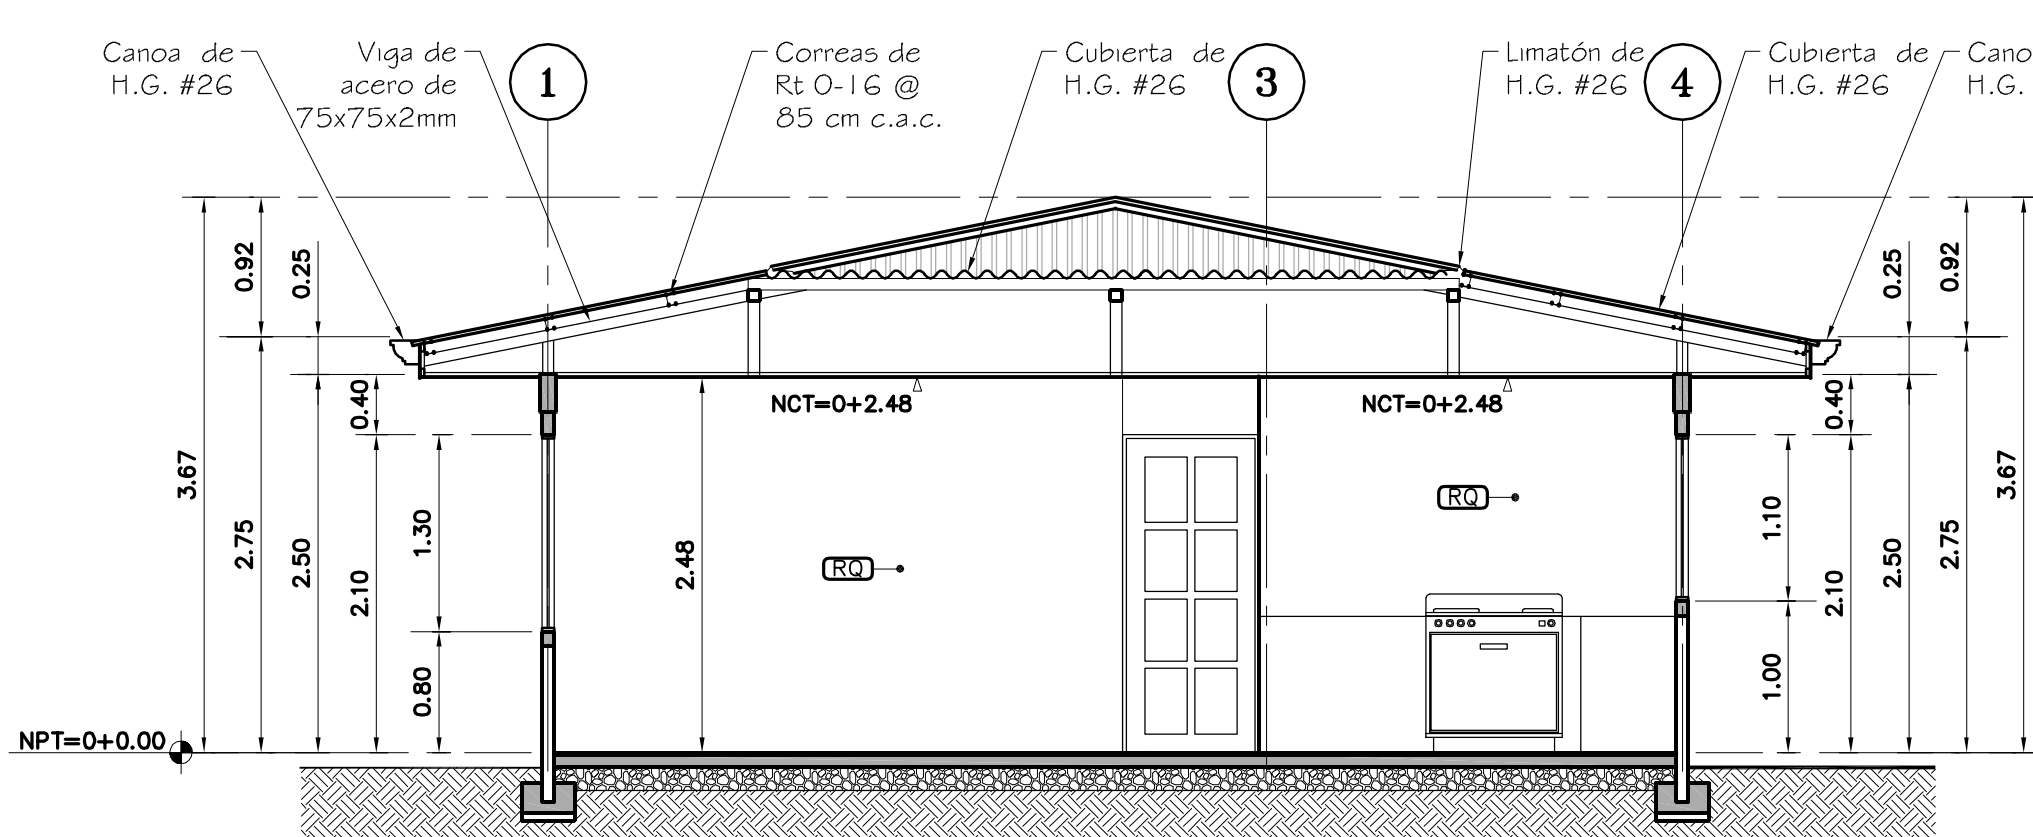

CORTE A-A. ESC 1:50

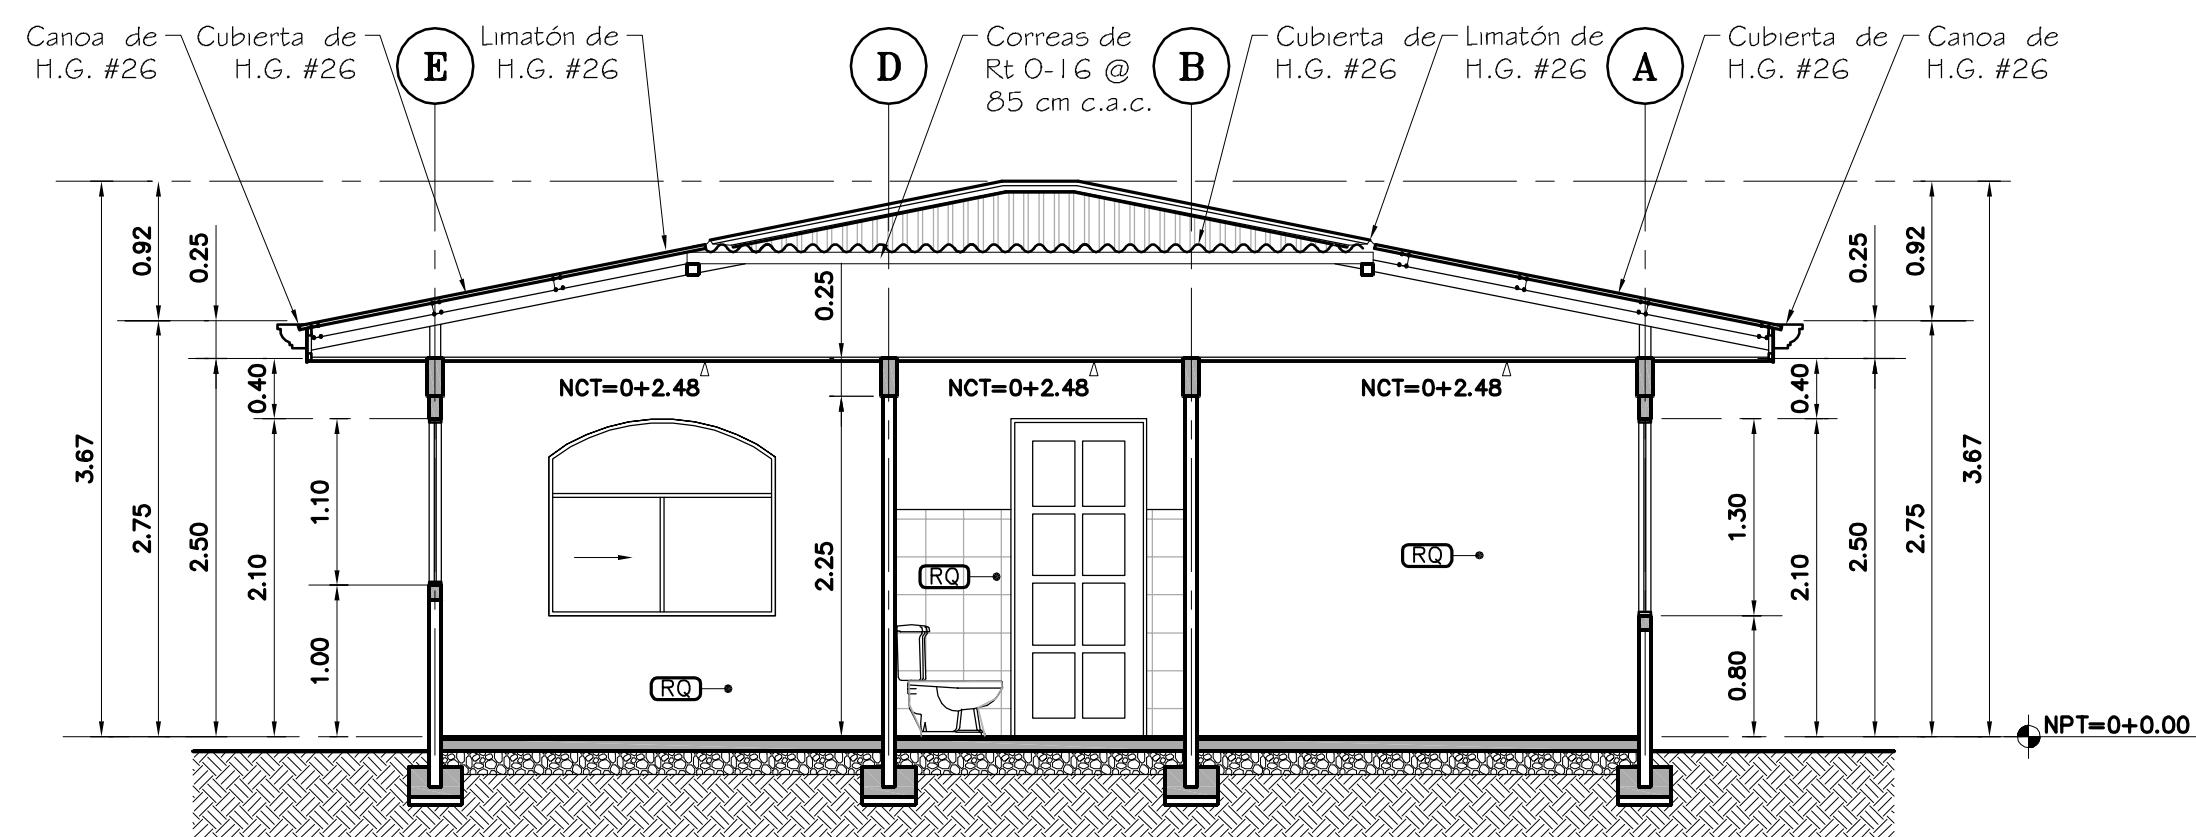

CORTE B-B. ESC 1:50

SIMBOLOGIA GENERAL ARQUITECTONICA

	INDICA MATERIAL DE CIELO		INDICA NUMERO DE CORTE		INDICA ACABADO DE PARED
	INDICA MATERIAL DE PISO		INDICA NUMERO DE LAMINA DONDE SE UBICA		INDICA SIMBOLO DE NIVEL DE PISO TERMINADO
	INDICA TIPO DE VENTANA		INDICA NUMERO DE SECCION PARED		INDICA NIVEL DE CIELO TERMINADO
	INDICA CAMBIO DE NIVEL EN PISO		INDICA NUMERO LAMINA DONDE SE UBICA		INDICA NIVEL DE CIELO TERMINADO


TABLA DE ACABADOS

	CIELO	PISO	PAREDES
GB	CIELOS DE GYPSUM ACABADO LISO Y PINTADO	AZ. AZULEJO DE 15 x 15 cm.	RQ. REPELLO QUEMADO CON PASTA Y PINTURA 2 MANOS
		CER. CERAMICA DE 33 x 33 cm	A.Z. AZULEJO DE 15 x 15 cm.

SIMBOLOGIA PLUVIAL

	TUBERIA AGUA PLUVIAL P.V.C. 100 mm. #. S.D.R. 32.5 1% DE PENDIENTE.
	REGISTRO PLUVIAL CON REJILLA (VEASE DETALLE LAMINA 6/8).
	BAIANTE AGUA PLUVIAL EN PVC 75 mm. #.
	DESCARGA DE AGUA PLUVIAL.
	INDICA DIRECCION DE FLUJO EN TUBERIA Y/O CANOA.

TANQUE SEPTICO Y DRENAJE SEGUN NORMAS DEL MINISTERIO DE SALUD DE 18 ML.

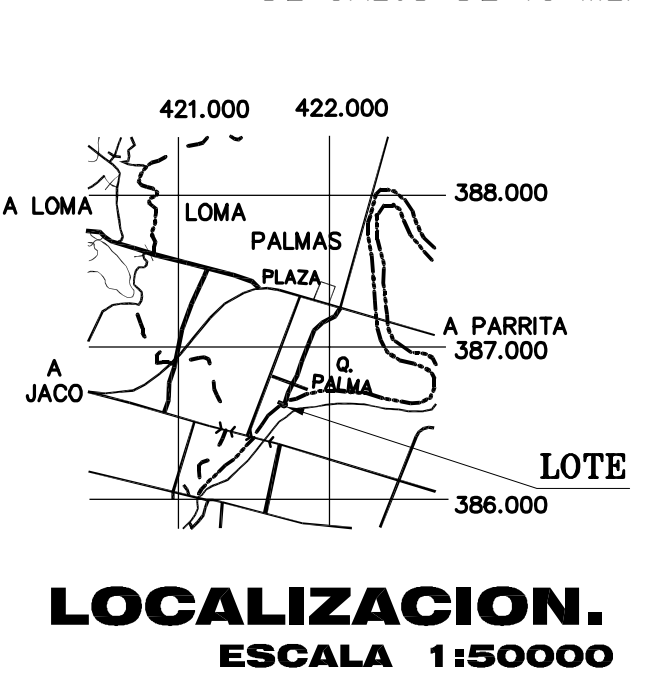

LOCALIZACION. ESCALA 1:50000

UBICACION. ESCALA 1:1000

PROYECTO:

PROPIETARIO:

PROVINCIA	CANTON	DISTRITO
-----------	--------	----------

COLABORÓ:

DISEÑO:

DIBUJO:

PROFESIONAL RESPONSABLE:

FIRMA: No. REG.

PROFESIONAL RESPONSABLE EJECUCION DE OBRA:

FIRMA: No. REG.

INFORMACION REGISTRO PUBLICO:

PROPIETARIO:

No. CATASTRO:

SITAS: ES PARTE DEL FOLIO REAL

CONTENIDO:

PLANTA DE DISTRIBUCION ARQUITECTONICA
ELEVACIONES Y CORTES A-A Y B-B
TABLA DE ACABADOS, SIMBOLOGIA GENERAL
UBICACION Y LOCALIZACION.

ESCALA	FECHA	LAMINA No.
--------	-------	------------

1 DE 2