



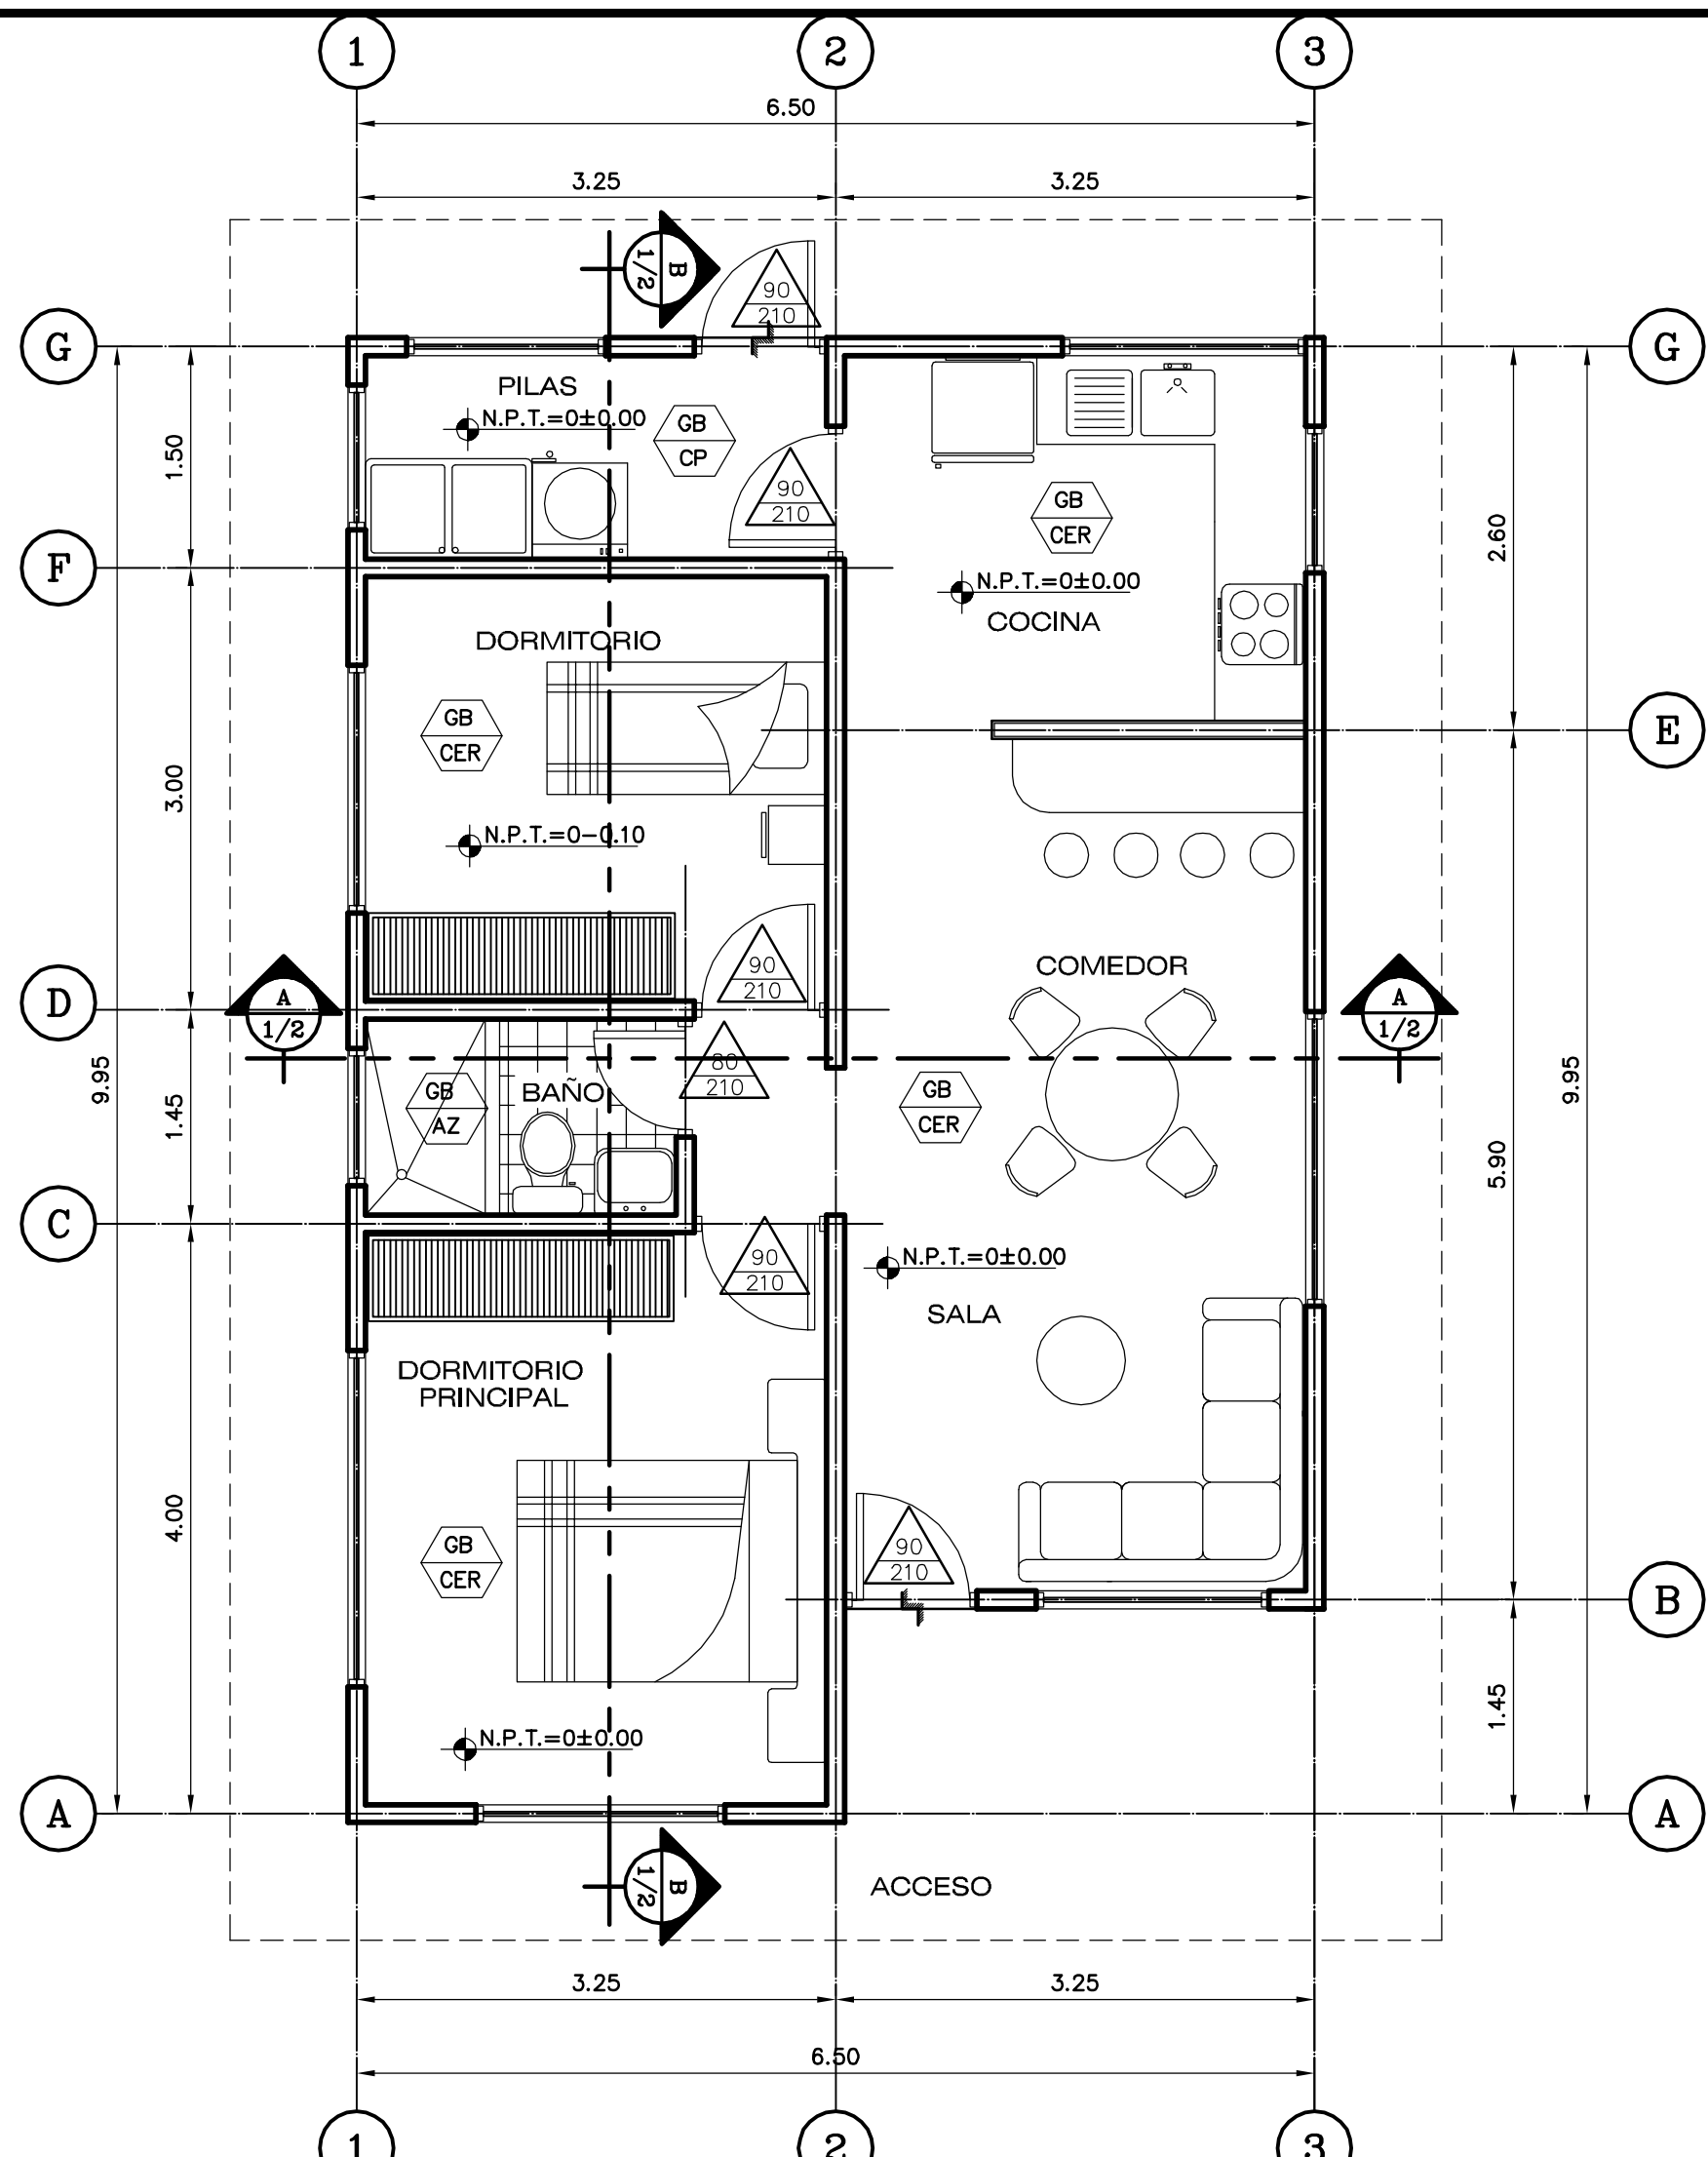


PLANTA DE DISTRIBUCION

ESCALA 1 : 50

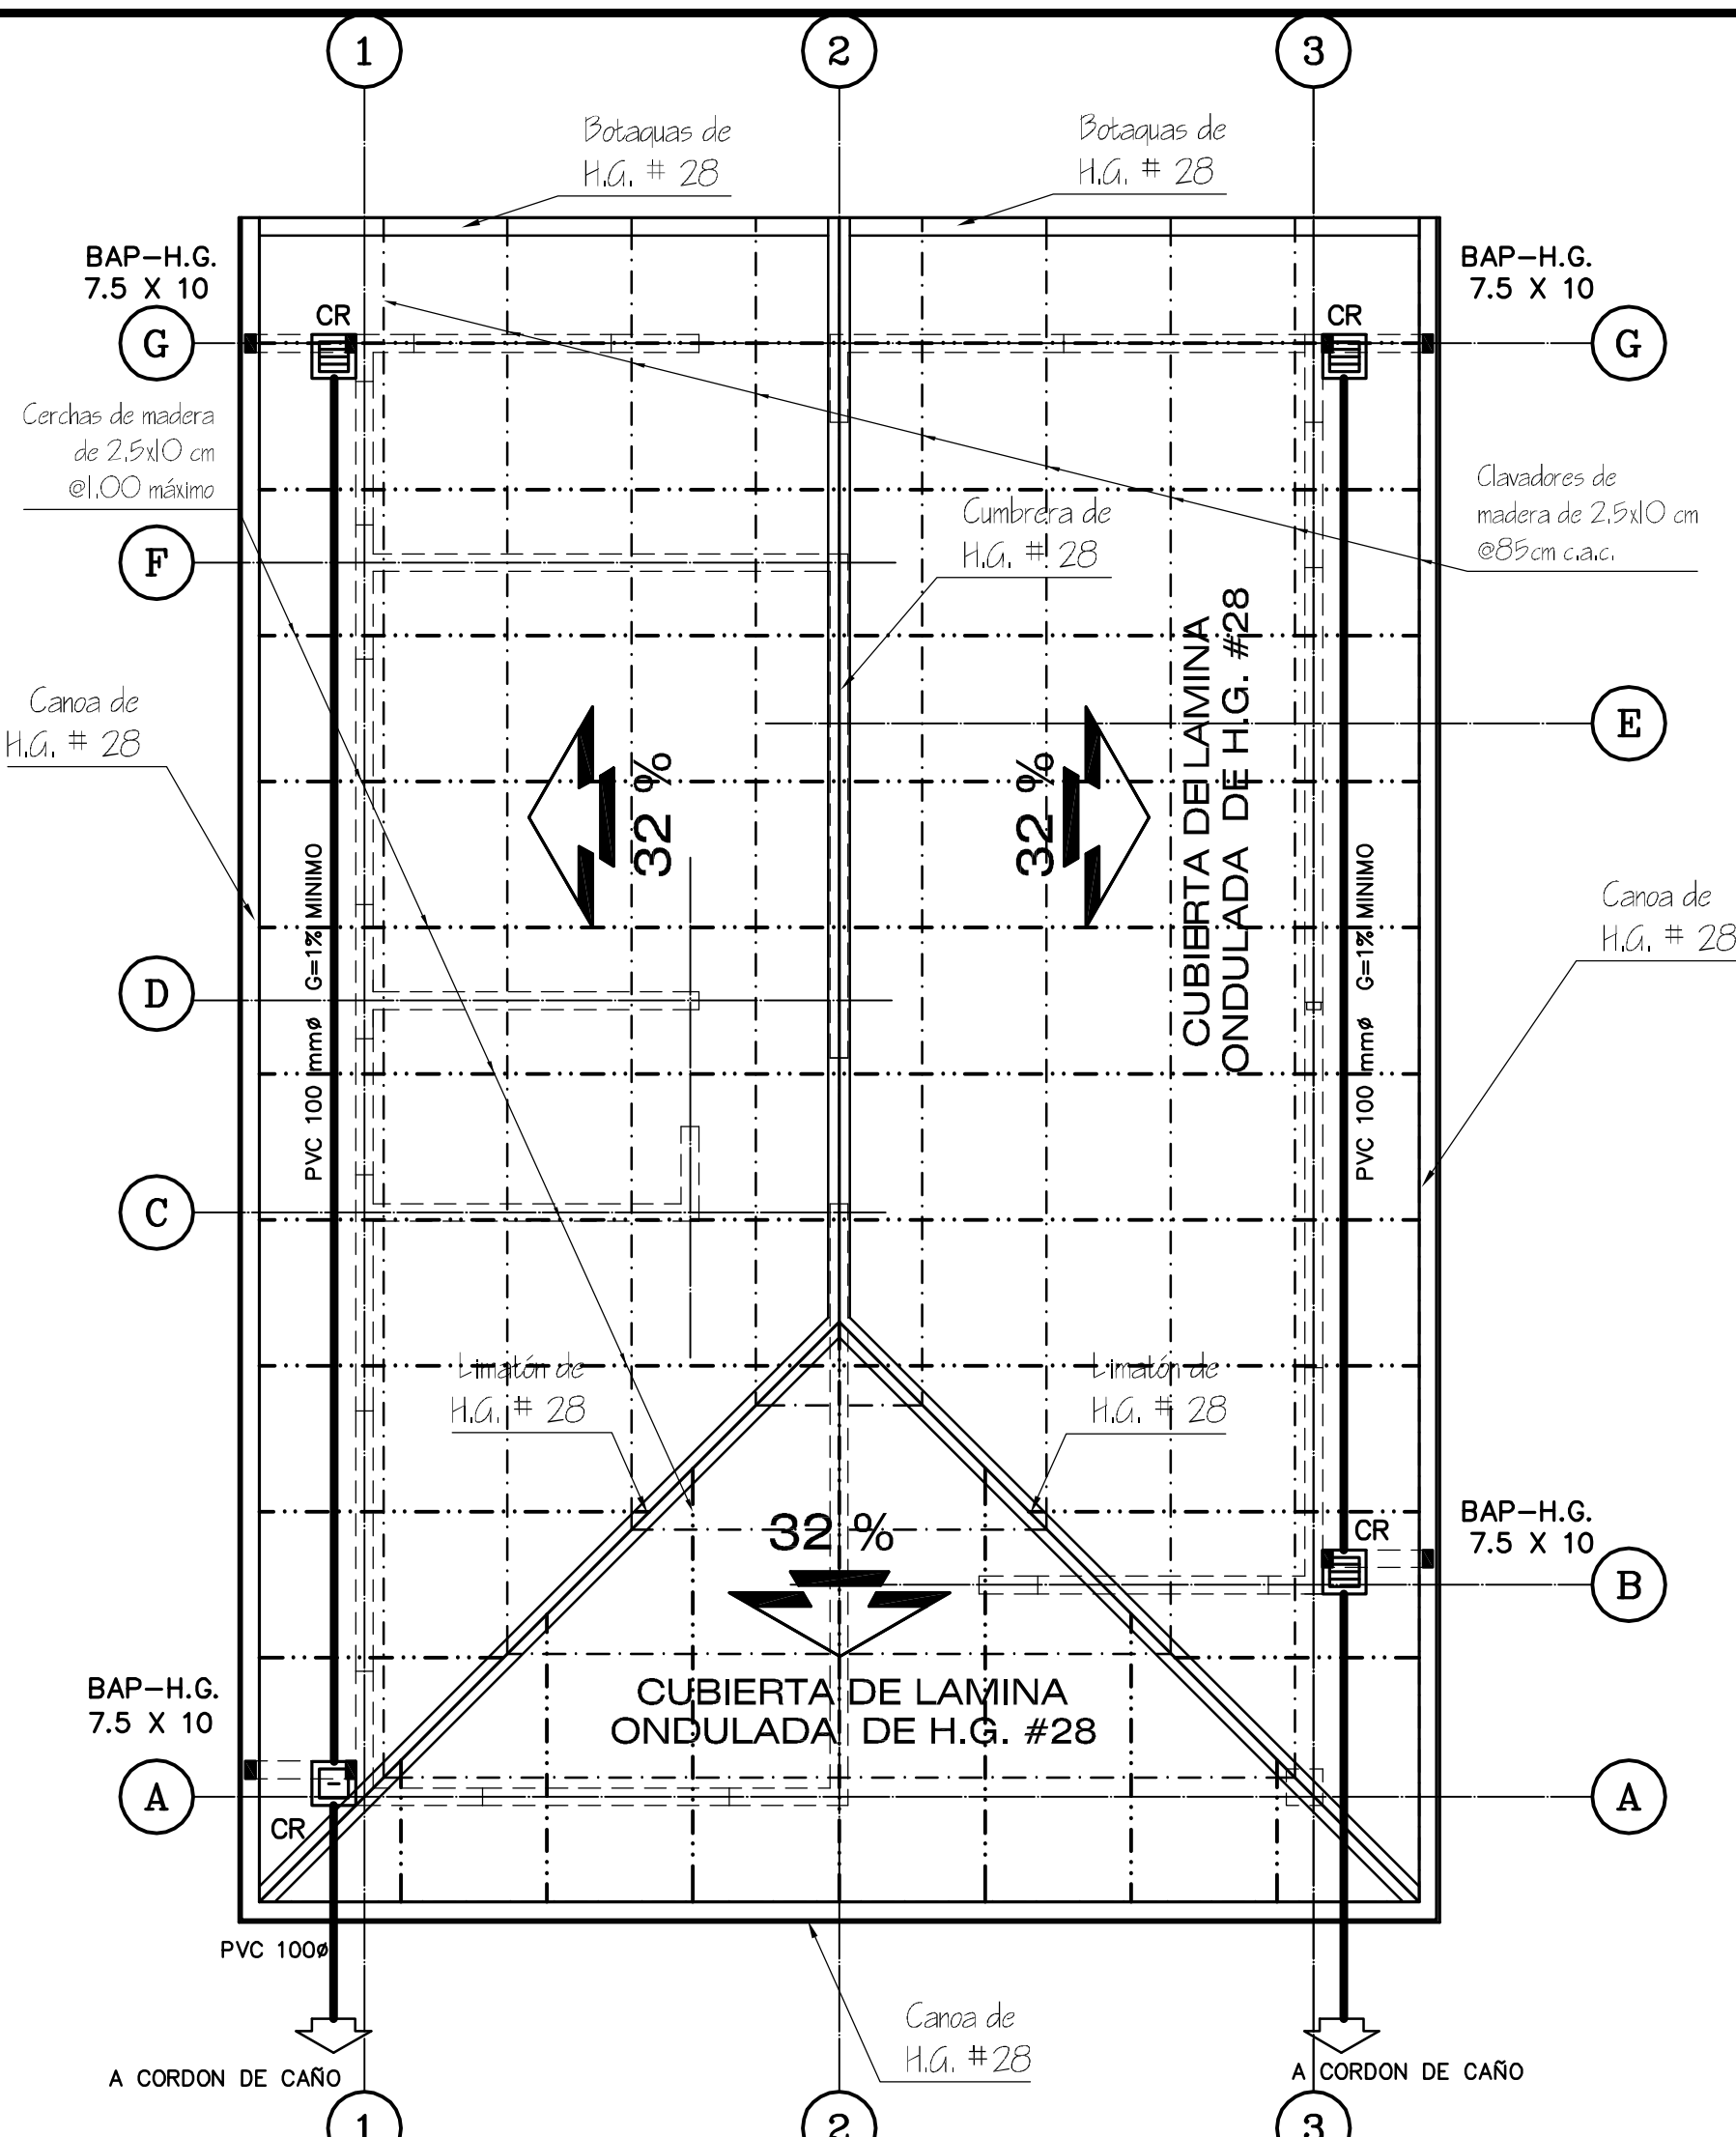


PLANTA DE TECHOS Y PLUVIALES

ESCALA 1 : 50

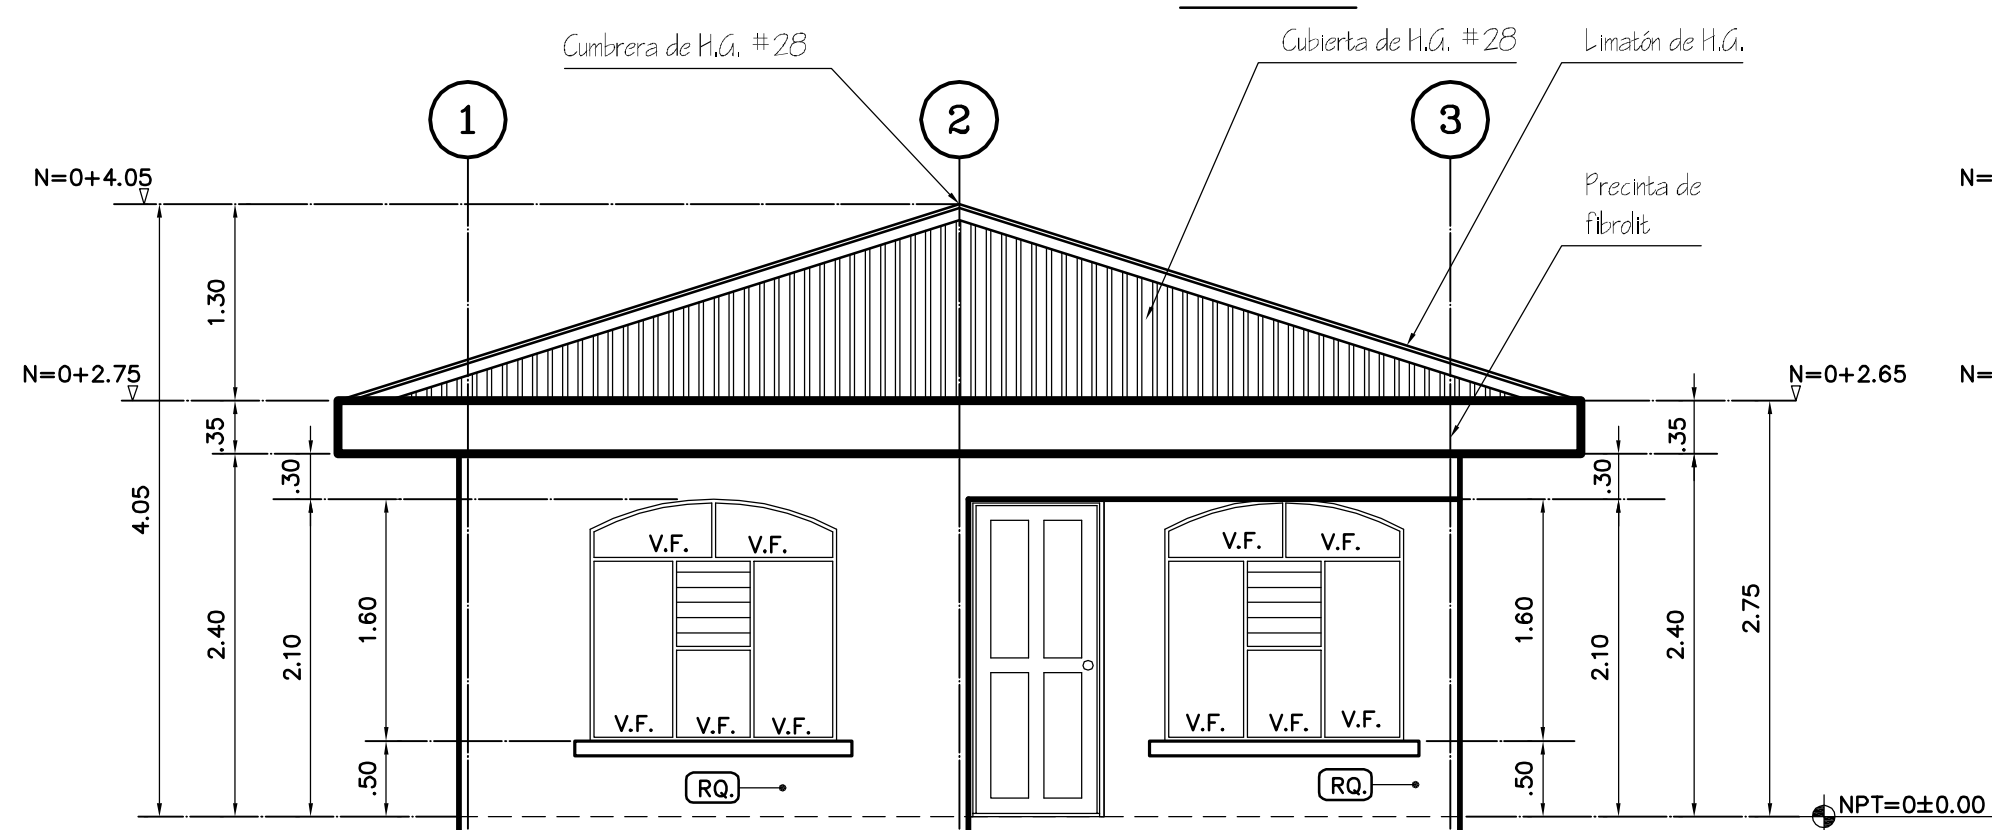


ELEVACION FRONTAL

ESCALA 1 : 50

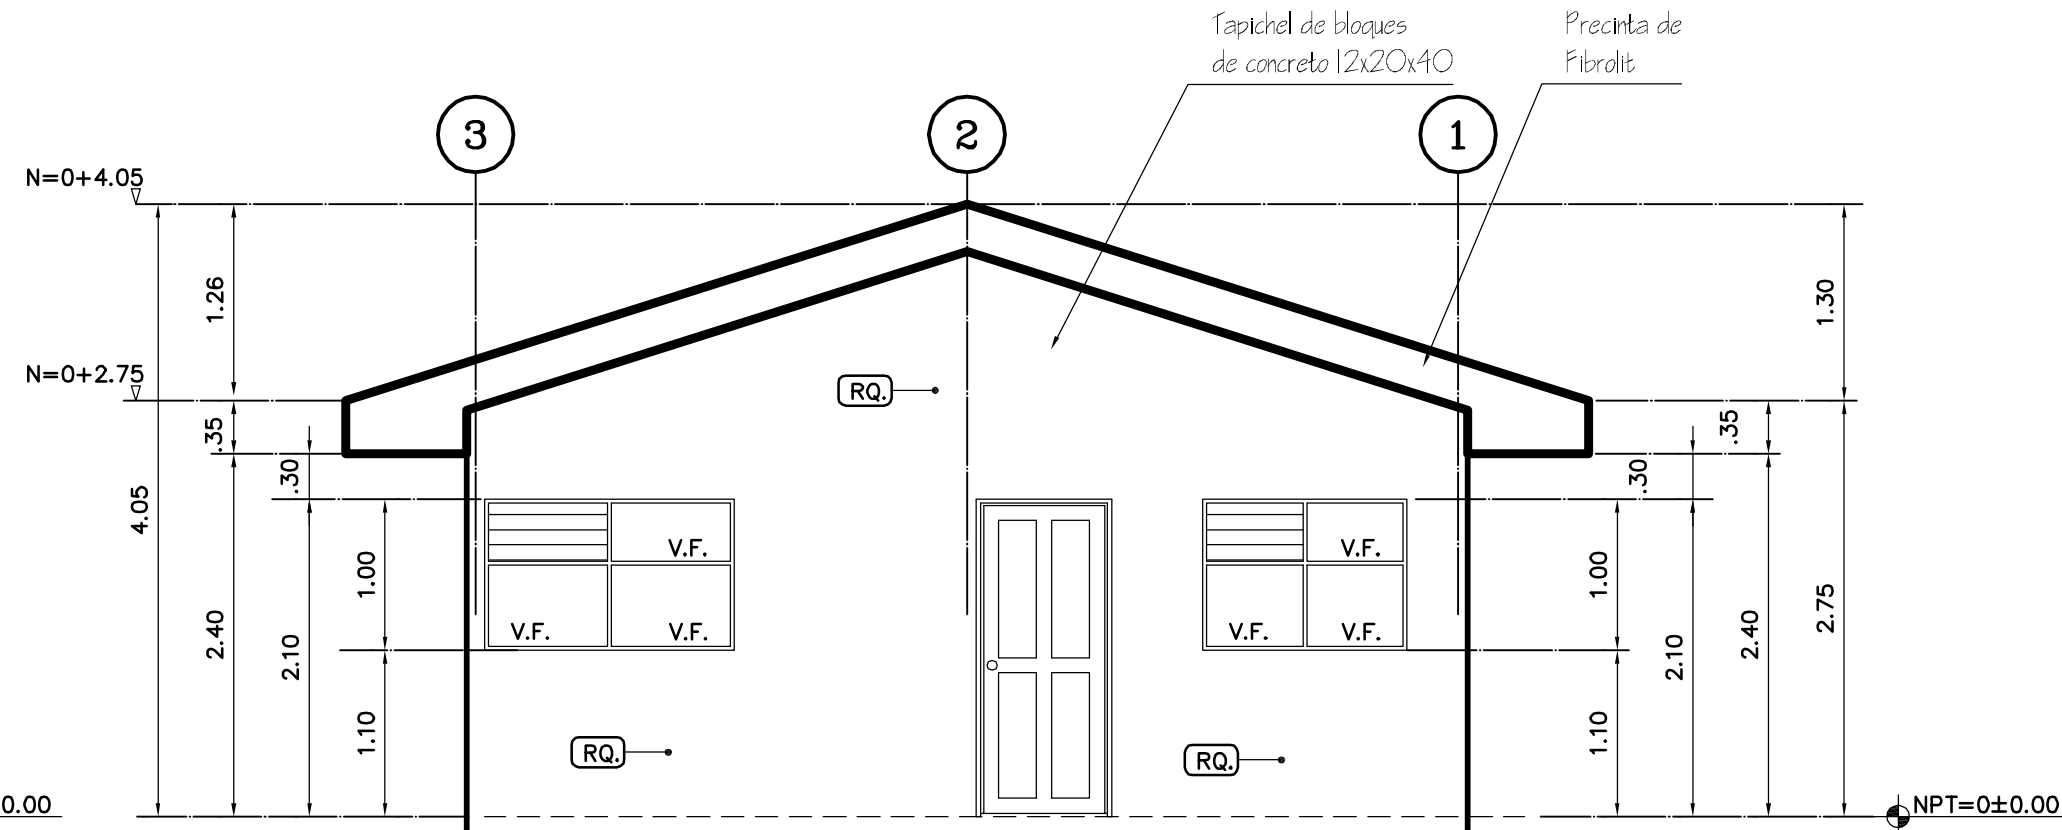


ELEVACION POSTERIOR.

ESCALA 1 : 50

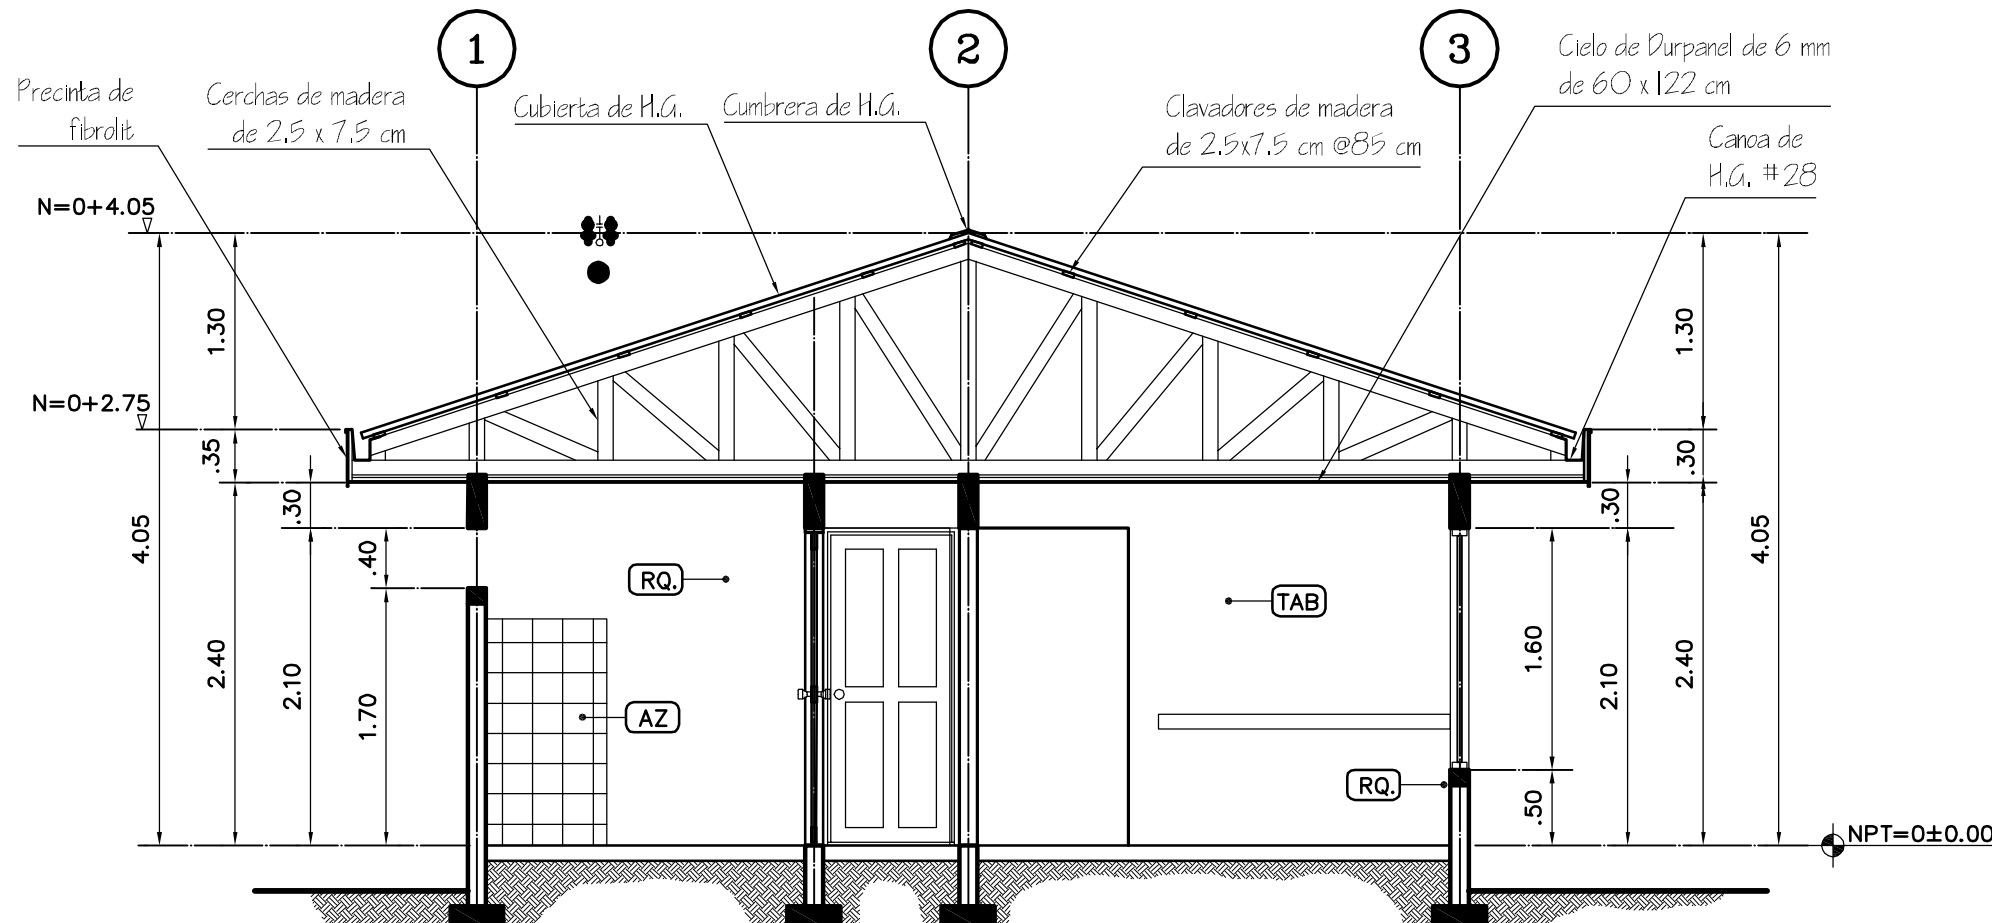

CORTE A - A

ESCALA 1 : 50

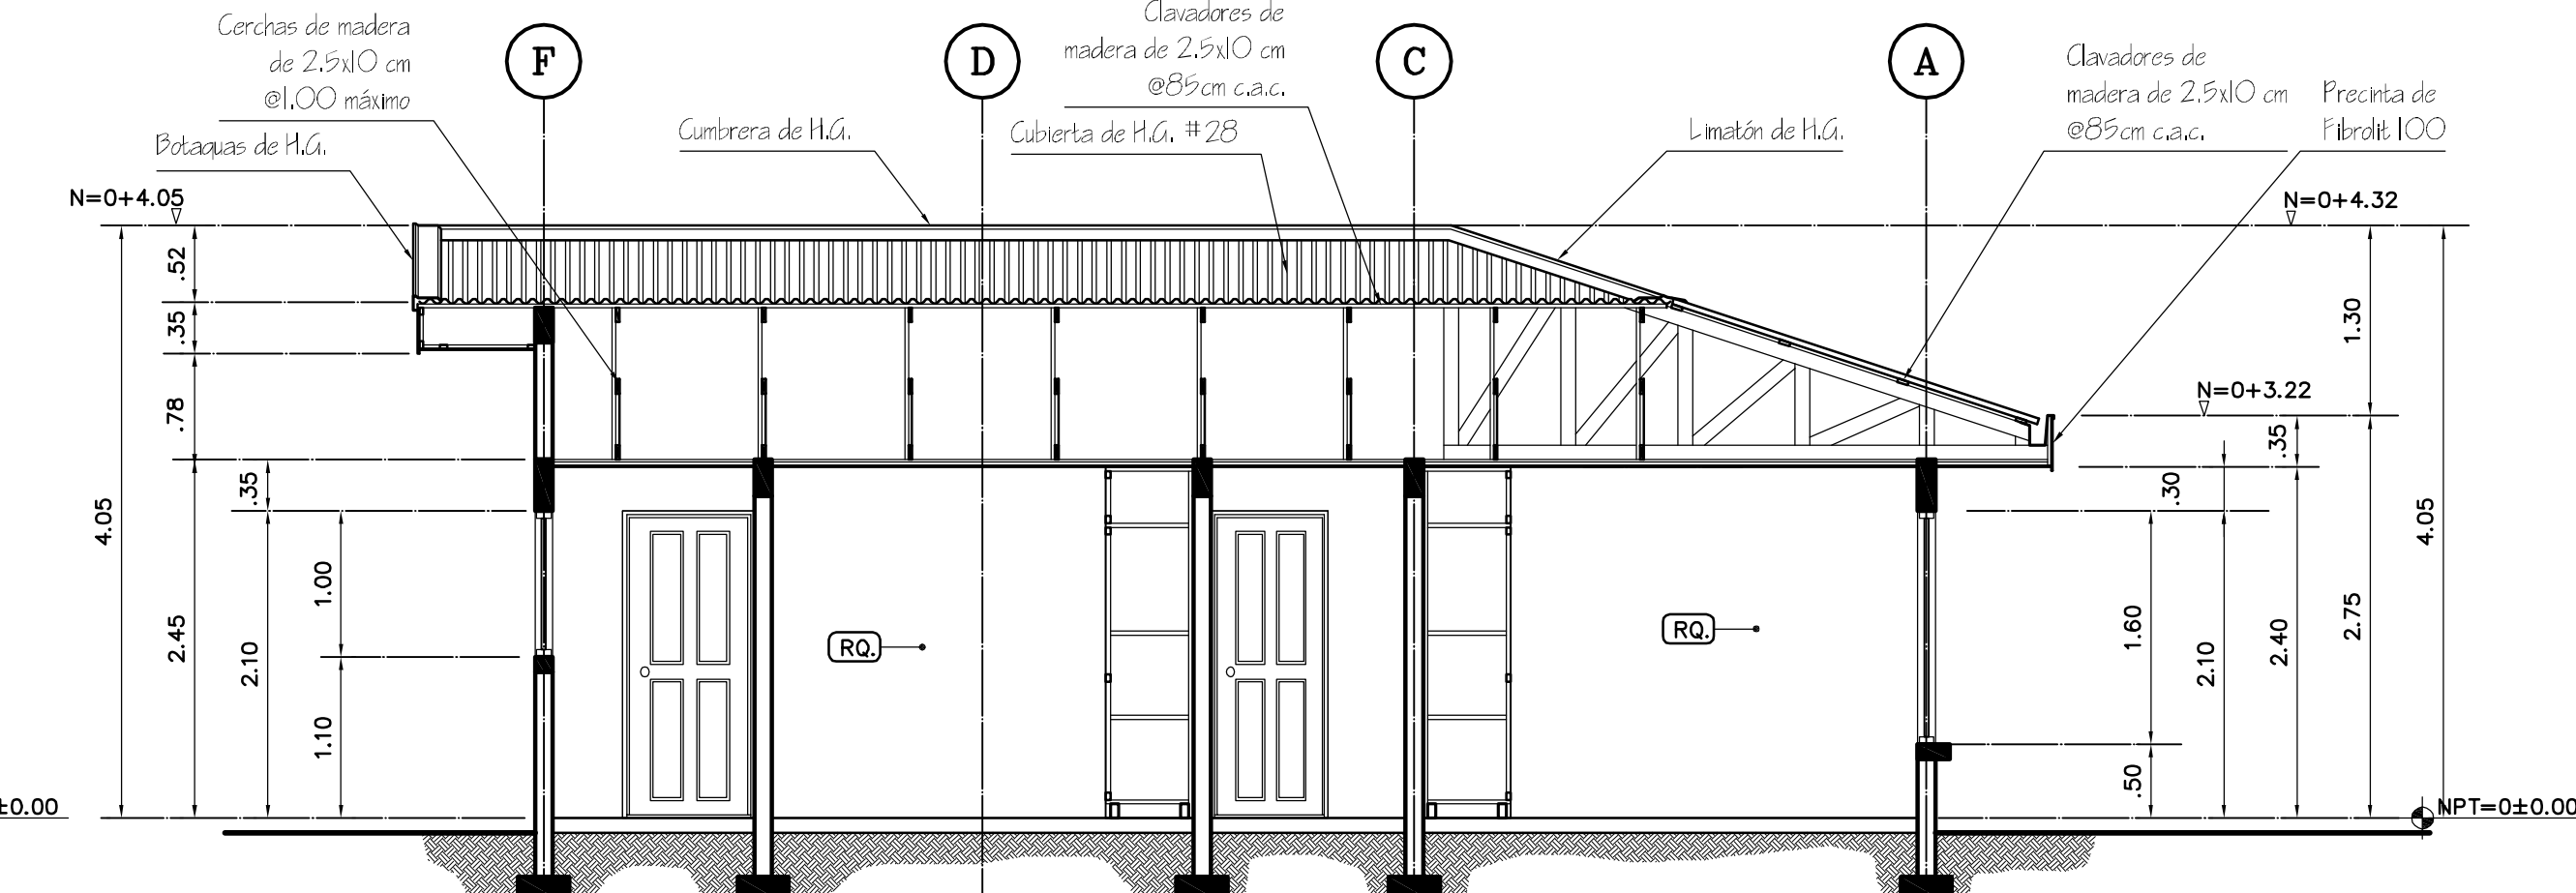


CORTE B - B

ESCALA 1 : 50



LOCALIZACION
ESCALA 1:1000

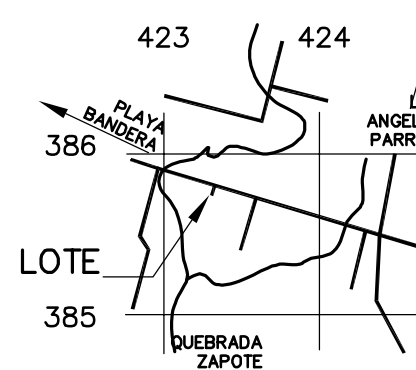

UBICACION
HOJA PARRITA
ESCALA 1:50.000

SIMBOLOGIA GENERAL
ARQUITECTONICA

- INDICA MATERIAL DE CIELO
- INDICA MATERIAL DE PISO
- INDICA TIPO DE VENTANA
- INDICA NUMERO DE CORTE
- INDICA NUMERO DE LAMINA DONDE SE UBICA
- INDICA NUMERO DE SECCION PARED
- INDICA NUMERO LAMINA DONDE SE UBICA
- INDICA CAMBIO DE MATERIAL DE PISO
- INDICA CAMBIO DE MATERIAL DE CIELO
- INDICA CAMBIO DE NIVEL EN PISO
- INDICA ACABADO DE PARED
- INDICA SIMBOLO DE NIVEL DE PISO TERMINADO
- INDICA NIVEL EN ELEVACION
- INDICA NIVEL DE CIELO TERMINADO

TABLA DE ACABADOS

CIELO	
GB	LAMINA DE GYPSUM BOAR DE 8MM
-	SIN CIELO
PISO	
CER	CERAMICA IMPORTADA DE 30 X 30 CM
ZAC	ZACATE (NEC)
AZ	AZULEJO
PAREDES	
R.Q.	REPELLO FINO
A.Z.	AZULEJO DE 15 X 15 CM.
FIB	FIBROLIT DE 8 mm

PROYECTO:

PROPIETARIOS:

PROVINCIA	CANTON	DISTRITO
-----------	--------	----------

ARQUITECTO:

COLABORO:

REVISO:

DIBUJO :

PROFESIONAL RESPONSABLE:

FIRMA: _____ No. REG. _____

PROFESIONAL RESPONSABLE DIRECCION TECNICA:

FIRMA: _____ No. REG. _____

INFORMACION REGISTRO PUBLICO:

PROPIETARIO:

No. CATASTRO:

SITAS: FOLIO REAL

CONTENIDO:

PLANTA BAJA DE DISTRIBUCION ARQUITECTONICA
PLANTA DE TECHOS Y PLUVIALES
FACHADAS Y CORTES
SIMBOLOGIA GENERAL Y TABLA DE ACABADOS
UBICACION Y LOCALIZACION